PL-01 — REPRISE EN SOUS-ŒUVRE RDC

Existant conservé, démolitions D1 à D6, appuis BA et profilés S355 — échelle 1/50

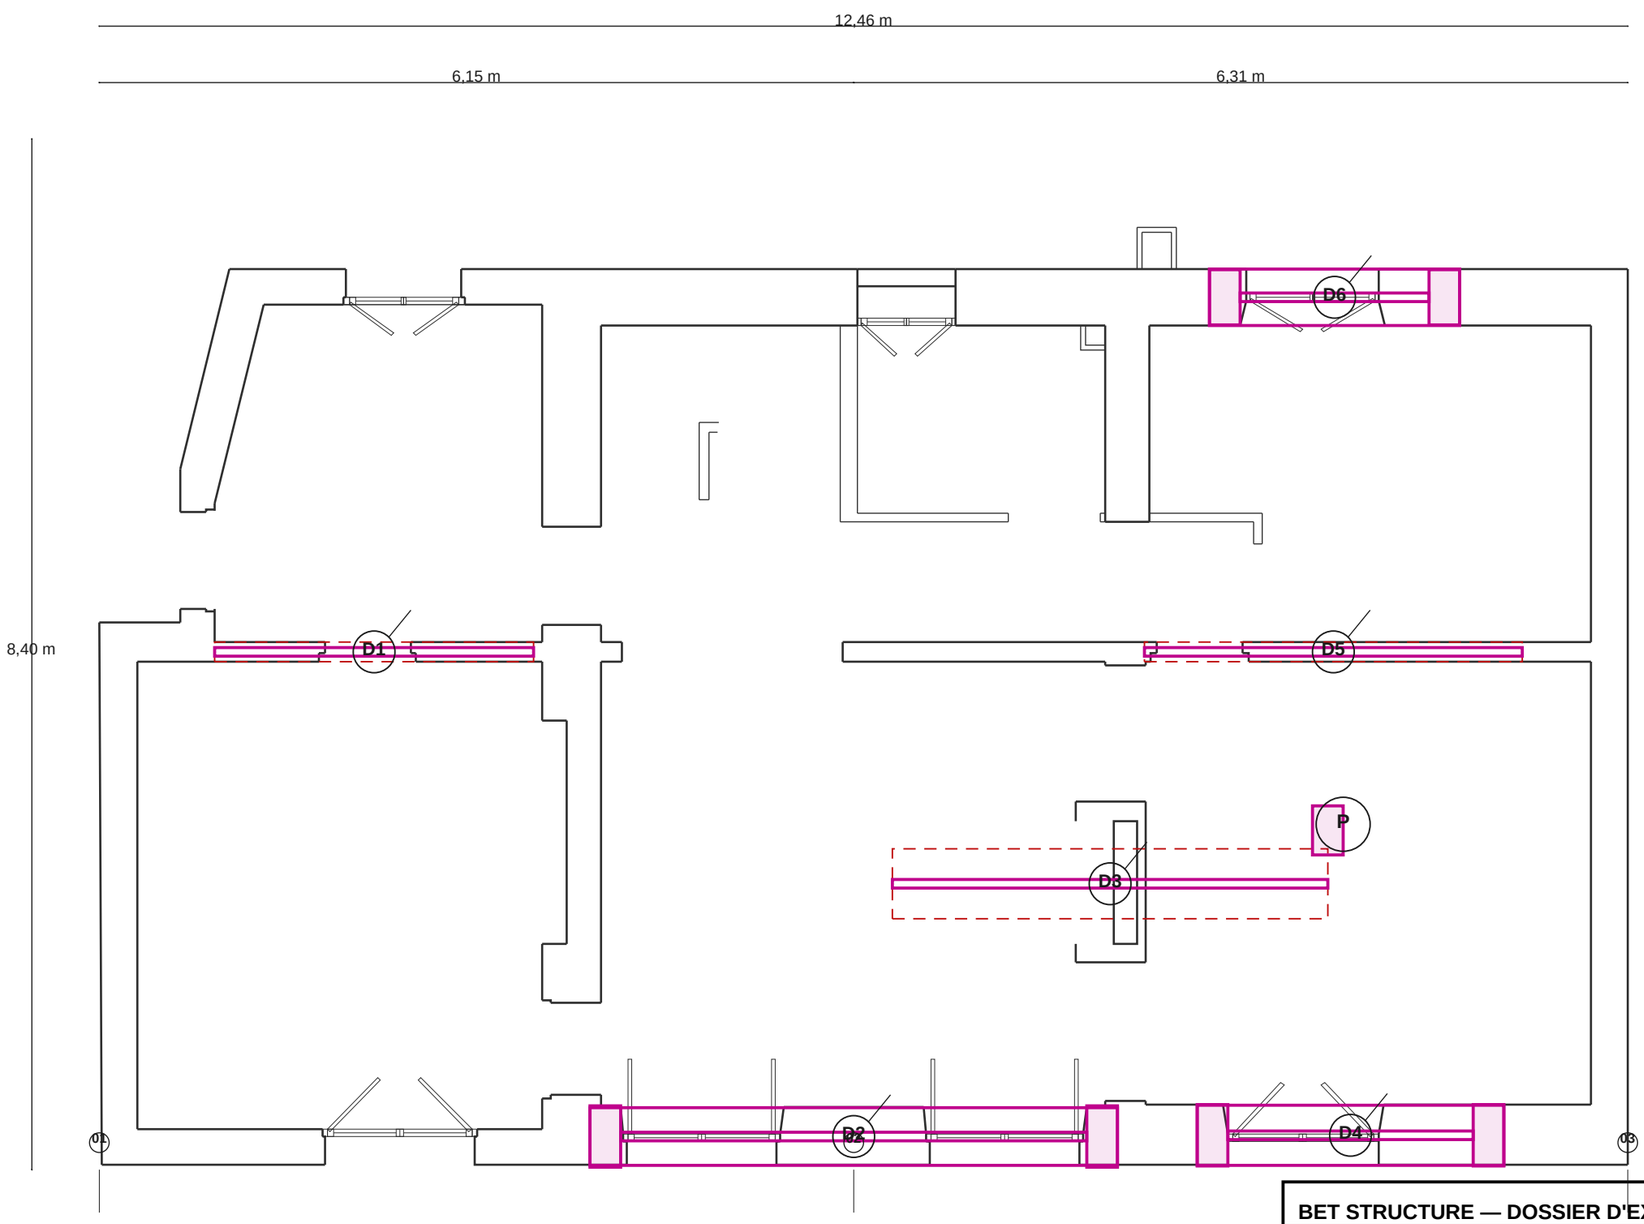

TRAPPES À LINGE (H-16)

Position estimée depuis les plans ; chaque trappe est entourée d'un nuage de révision.

Combles — 30 × 31 cm
x ≈ 46491 (relevé DXF)

R+1 — 30 × 31 cm
x ≈ 42890 (relevé DXF)

RDC — 30 × 31 cm
x ≈ 48491 (relevé DXF)

LÉGENDE

- Existant conservé
- Maçonnerie démolie (D1 à D6)
- Béton armé coulé en place
- Profilé métallique S355 jumelé
- Cotes, axes, nuage de révision

REPRISES EN SOUS-ŒUVRE D1 À D6

Rep.	Portée	Mur	Profilé
D1	2,60 m	16 cm	IPE 160
D2	3,80 m	47 cm	IPE 270
D3	3,55 m	57 cm	IPE 300
D4	2,00 m	49 cm	IPE 180
D5	3,08 m	16 cm	IPE 180
D6	1,54 m	46 cm	IPE 160

NOTES

1. Cotes en cm ; niveaux en m NGF (sol RDC 41,46).
2. Reprises D1 à D6 : profilés S355, matés au mortier sans retrait (contact ≥ 90 %). Jambages et sommiers BA C25/30.
3. Trappes à linge : position estimée (H-16), entourée d'un nuage de révision — ajustement après relevé de l'entraxe réel des solives, dans la zone de tolérance DOC-02 §6.2.
4. D1 : fondation filante meulière continue conservée (H-01).
5. Aucune démolition avant PV de résistance BA à 28 jours.

BET STRUCTURE — DOSSIER D'EXÉCUTION	**PL-01**
	Tâche 3 — plans généraux
Affaire GA-2026-58AIGLE — BET Structure 58 rue de l'Aigle — 92250 La Garenne-Colombes	Échelle : 1/50 A3 paysage
PL-01 — REPRISE EN SOUS-ŒUVRE RDC	Indice A — 11/11/2026
Existant, démolitions D1 à D6, appuis BA et profilés	Échelle 1/50