PL-02 — PLAN DE COFFRAGE DE L'EXTENSION

Terrasse accessible — voile mitoyen, poteau BA à 2,00 m, poutre-acrotère 30 × 67, puits et longrines — 1/50

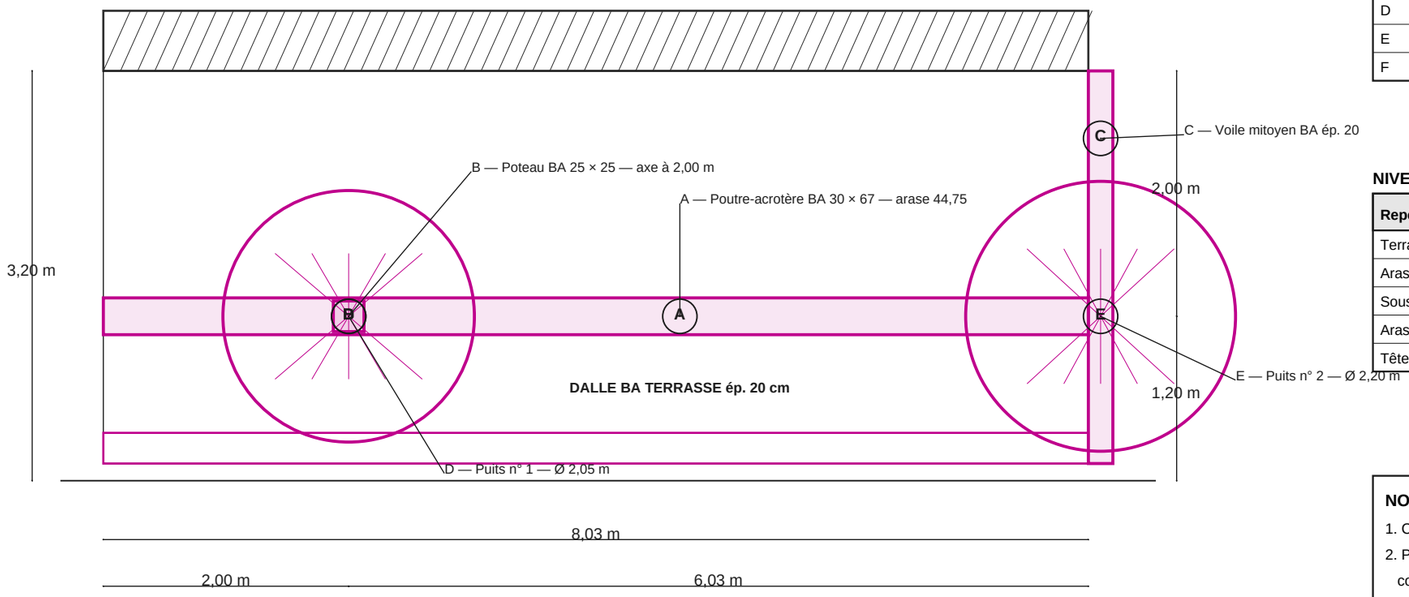

LÉGENDE

- Maçonnerie existante conservée
- Béton armé coulé en place (coffrage)
- Cotes, repères, axes

REPÉRAGE

Rep.	Désignation	Section
A	Poutre-acrotère	30 × 67
B	Poteau BA verrière	25 × 25
C	Voile mitoyen	ép. 20
D	Puits n° 1	Ø 205
E	Puits n° 2	Ø 220
F	Dalle terrasse	ép. 20

NIVEAUX NGF

Repère	Altitude
Terrain / sol RDC	41,11 / 41,46
Arase fondations	39,02
Sous-face plancher RDC	44,08
Arase acrotère	44,75
Tête verrière	45,90

NOTES

1. Cotes en cm ; niveaux en m NGF (DOC-03 §1).
2. Poutre-acrotère : 4 HA 20 + étriers HA 8 e = 175, contre-flèche de coffrage 20 mm.
3. Poteau 25 × 25 : 6 HA 8, cadres HA 8 e = 200.
4. Puits descendus à NGF 39,02 (assise des fondations existantes) — béton C16/20 coulé en pleine fouille.
5. Voile mitoyen : 4 HA 12 par face + HA 8 e = 250.
6. Joint de dilatation 20 mm entre extension et façade.

BET STRUCTURE — DOSSIER D'EXÉCUTION	**PL-02**
	Tâche 3 — plans généraux
Affaire GA-2026-58AIGLE — BET Structure 58 rue de l'Aigle — 92250 La Garenne-Colombes	Échelle : 1/50 A3 paysage
PL-02 — PLAN DE COFFRAGE DE L'EXTENSION	Indice A — 11/11/2026
Voile mitoyen, poteau BA, poutre-acrotère 30 × 67, puits et dalle de terrasse	Échelle 1/50