PL-03 — COUPES ET ÉLÉVATIONS DE L'EXTENSION

Coupe verticale sur la terrasse (1/50) et détail d'appui de la poutre-acrotère (1/20)

COUPE VERTICALE A-A SUR LA TERRASSE — 1/50

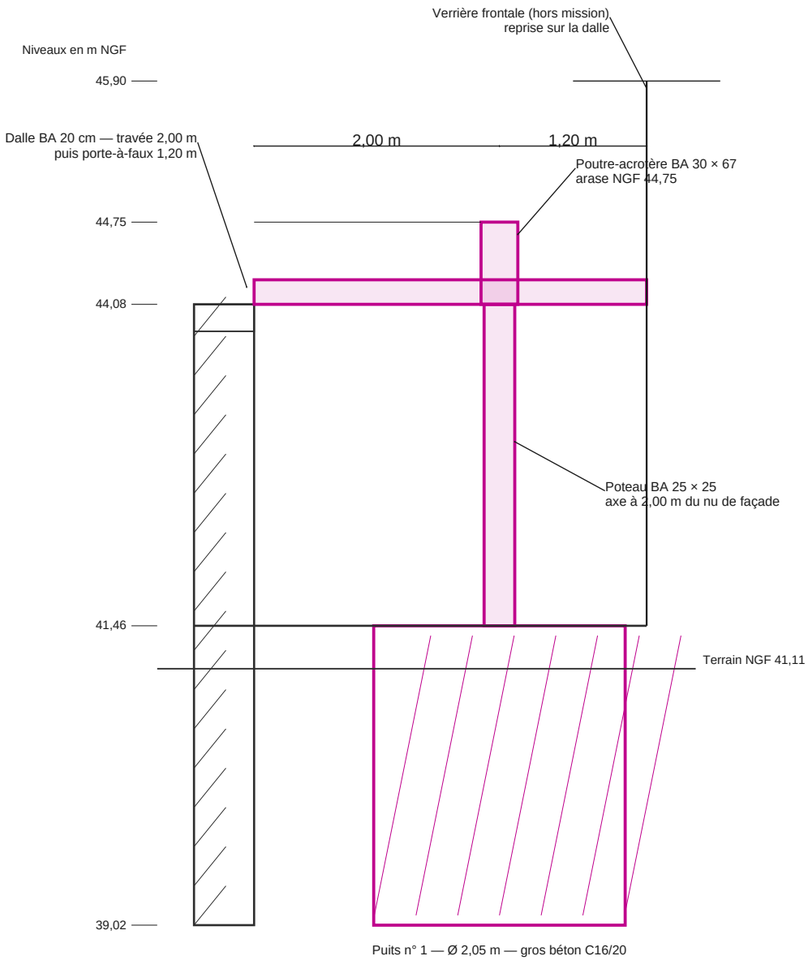

DÉTAIL D'APPUI POUTRE / POTEAU — 1/20

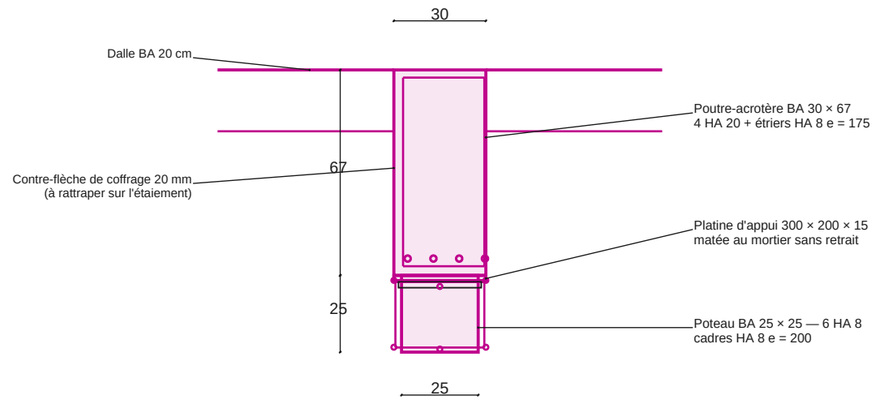

LÉGENDE

- Béton armé coulé en place
- Platine / appareil d'appui S275
- Armatures B500B
- Maçonnerie existante conservée

NOTES

1. Niveaux en m NGF ; sol fini RDC = 41,46 (DOC-01 §5).
2. La poutre-acrotère fait office d'acrotère : arase 44,75, sous-face 44,08 (sous-face du plancher haut RDC).
3. Poteau BA 25 × 25 à 2,00 m du nu de façade (arbitrage E-01).
4. Contre-flèche de coffrage 20 mm sur la poutre-acrotère.
5. Appui glissant sur le voile mitoyen (armatures en attente).
6. Fondations descendues à NGF 39,02 (assise de l'existant).

BET STRUCTURE — DOSSIER D'EXÉCUTION	**PL-03**
	Tâche 3 — plans généraux
Affaire GA-2026-58AIGLE — BET Structure 58 rue de l'Aigle — 92250 La Garenne-Colombes	Échelle : 1/50 A3 paysage
PL-03 — COUPES ET ÉLÉVATIONS DE L'EXTENSION	Indice A — 11/11/2026
Coupe verticale sur la terrasse (1/50) et détail d'appui de la poutre-acrotère (1/20)	Échelle 1/50 et 1/20