
CROISSY-FLORA — B-25 (Ind. E) — CONTREVENTEMENT, TORSION ET JOINTS — STABILITÉ EN SERVICE
PRINCIPE — NE PAS EXÉCUTER — Indice P (ni vérification sismique D-26, ni stabilité provisoire D-27)

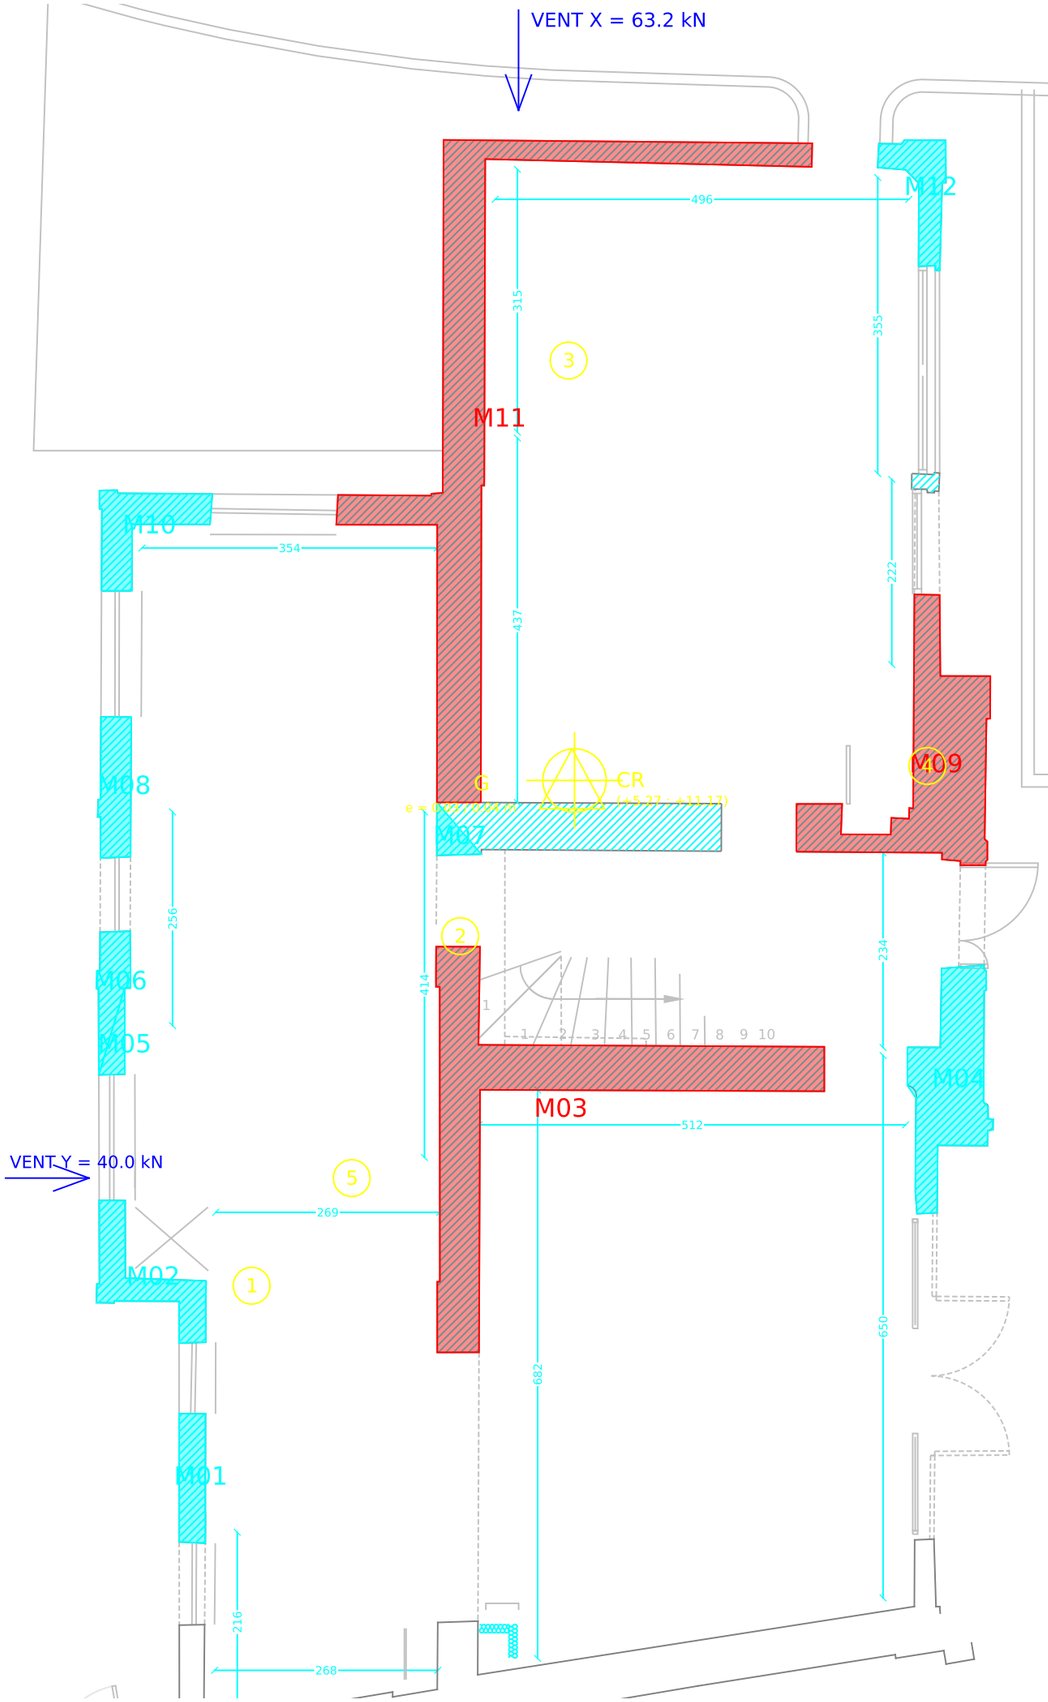

PRINCIPE — NE PAS EXECUTER — Indice P (B-25 Ind. E)

1. SYSTEME DE CONTREVENTEMENT — VERDICT

La maçonnerie porteuse existante, et elle seule — DECISION D-29 du 20/10/2026.
12 voiles comptes au RDC · 9 au R+1 · ΣKx = 1,21 GN/m · ΣKy = 1,64 GN/m
EXCLUS : frangements F1a/b/c, F2, F3, F4 · renforts R1/R2/R3/Stab1
poteaux P1-N/S, P2, P3, J1 · charpente · planchers (diaphragme flexible)
cloisons / doublages / isolants (V9 : jamais sur une vue structurelle)

2. VOILES COMPTES AU RDC — RAIDEURS HORIZONTALES

ID	A(m²)	L(m)	t_eq(m)	Kx(kN/m)	Ky(kN/m)
M01	0.49	1.57	0.31	662	13521
M02	0.80	2.04	0.39	21180	20005
M03 *	4.58	5.19	0.88	525216	439310
M04	1.76	3.06	0.57	17609	100161
M05	0.16	1.08	0.15	144	1518
M06	0.42	1.76	0.24	771	9426
M07	0.17	0.81	0.21	438	604
M08	0.62	1.71	0.36	1139	19627
M09 *	2.79	3.28	0.85	113878	192477
M10	0.79	1.65	0.48	16859	12758
M11 *	5.49	9.07	0.60	503490	815171
M12	0.60	1.65	0.37	3620	16653

* voile majeur (M03 + M11 = 86 % de la raideur RDC)

REPERES DE LA PLANCHE

1 R-1 : F2 + F3 supprimes -> fonction horizontale perdue, non reconstituee
2 R-2 : F1a perce le refend 50 cm -> voile scinde en 2 trumeaux
3 M11 voile majeur RDC (815 171 kN/m en Y) — grandeur transmise a la MOE
4 M09 voile majeur RDC cote Est (192 477 kN/m en Y) — idem M03
5 CR / G du RDC — ecart e_struct = 0,04 m (X) / 0,03 m (Y)

3. TORSION ET VERIFICATION SOUS VENT (EC1 / EC6)

G = (+5.24 ; +11.13) m · CR = (+5.27 ; +11.17) m
e_struct : 0.04 m (vent X) · 0.03 m (vent Y)
e_accidentelle = ± 0,05 L = ± 0,87 m (X) · ± 0,55 m (Y) → elle gouverne
Mt = 28.6 kN·m (X) · 11.6 kN·m (Y)
fvk = (0,15 + 0,4 x 0,30) / 2,5 = 108 kPa
tau/fvk max = 0.028 → CAPACITE LARGEMENT TENUE

4. JOINTS DE DILATATION — AUCUN JOINT

Emprise 11,1 x 17,5 m · dilatation libre 5,2 mm · maçonnerie stabilisee
Frangements appuyes (portee <= 4,88 m) : aucune reprise de dilatation
-> D-28 consignee le 20/10/2026 : aucun joint · a reexaminer si l'emprise est modifiee

5. PHASE PROVISOIRE — HORS MISSION (D-27)

La verification du contreventement en phase provisoire incombe a la
maitrise d'oeuvre structure de conception (batiment existant).
AUCUNE verification provisoire n'est produite par nos soins.
Grandeurs transmises a la MOE (T-04) :
R+1 4 voiles majeurs = 88.9 % de la raideur totale
M08, M03, M09, M02
RDC 4 voiles majeurs = 95.1 % de la raideur totale
M11, M03, M09, M04
Restent de notre lot : etaiement d'execution (H-20) · mode operatoire
de pose · ordre F3 avant F2 · etaiement lateral des pignons (securite)

6. POSITION SISMIQUE — NON VERIFIEE (D-26)

Zone 1 (Ile-de-France) · seisme tres faible.
Arrete du 22/10/2010, art. 3 : aucune categorie d'importance n'est
soumise aux regles EC8 en zone 1 -> EC8 NON APPLICABLE.
DECISION CLIENT : aucune verification sismique produite, ni reglementaire,
ni de sensibilite. H-24 (sol C, agr 0,40) est neutralisee, non supprimee.

7. POINTS D'ARRET OUVERTS

PA-01 reconnaissance contradictoire de la continuite des voiles
M11/M03/M04 · M08/M03/M09 · trumeau M05 — AVANT TOUTE DEMOLITION
PA-02 verification de la liaison charpente-maconnerie des pignons — AVANT DEPOSE

8. MACONNERIE — HYPOTHESE D'ETUDE A CONFIRMER (D-34)

f_k = 1,5 MPa · E = 1 500 MPa · f_vk0 = 0,15 MPa : valeurs retenues pour nos etudes.
Leur confirmation par essais est HORS MISSION et a la charge du maitre d'ouvrage.
Essais non concluants -> reprise des etudes chiffree en prestation complementaire.

PRESCRIPTION OBLIGATOIRE D-09 (REPRODUCTION INTEGRALE) :
« AU MEME NIVEAU QUE LES FONDATIONS EXISTANTES... RAJOUTER DU GROS BETON...
CETTE NOTE EST A INDIQUER SUR LES PLANS ET NOTE DE CALCULS »
0,00 RELATIF = plancher bas du RDC (D-20/D-21) · arase -1,00 m/TN mini (D-08/D-12) · 60x60 mini (D-14) · SF1 80x80 (D-30)

EHPAD LA ROSERAIE — PAVILLON FLORA (CROISSY-SUR-SEINE)

SCHEMA DE CONTREVENTEMENT — STABILITE GLOBALE (PH RDC)

Brique B-25 · Indice E · 20/10/2026 · Mode HYPOTHESE-NOTIFIEE · Regime OUTILLE (V13)

Fond B-32 Ind. D · Echelle 1/80 · Unites DXF cm · Repere B-30 (P1)

PRINCIPE — NE PAS EXECUTER — Indice P