PL-02 — PLAN DE COFFRAGE DE L'EXTENSION

Terrasse 8,03 × 2,00 m — voile de rive sur semelle filante, poutre-acrotère isostatique, console 0,70 m — 1/50

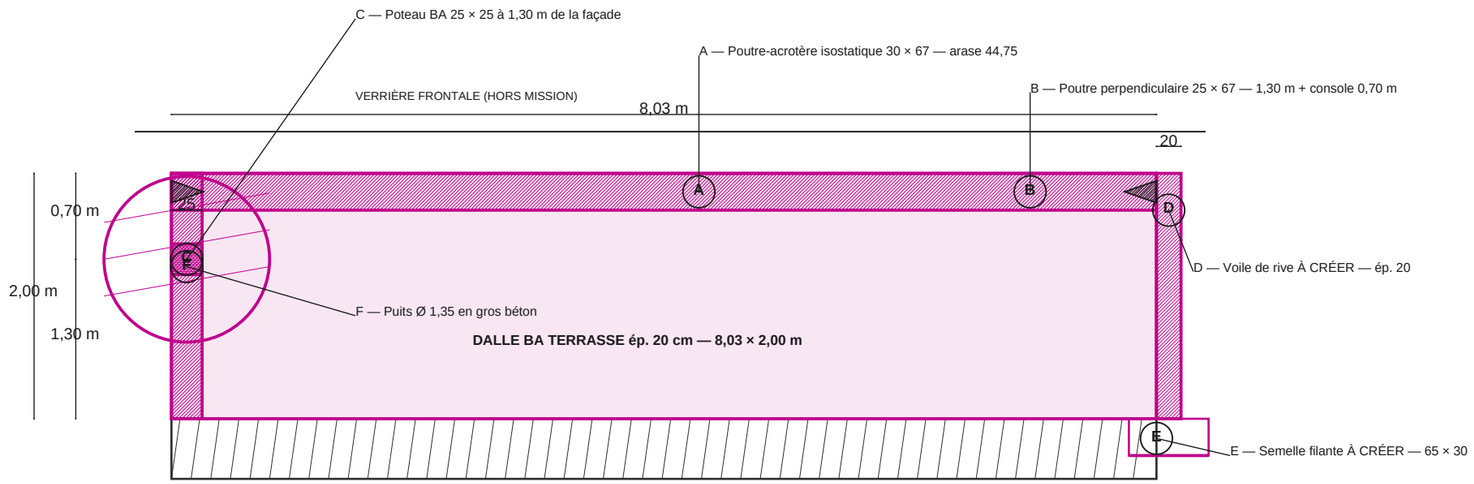

LÉGENDE

- Maçonnerie existante conservée
- Béton armé à créer (coffrage)
- Cotes, repères, axes

REPÉRAGE

Rep.	Désignation	Section
A	Poutre-acrotère isostatique	30 × 67
B	Poutre-acrotère perpendiculaire	25 × 67
C	Poteau BA	25 × 25
D	Voile de rive (à créer)	ép. 20
E	Semelle filante (à créer)	65 × 30
F	Puits de gros béton	Ø 135
G	Dalle terrasse	ép. 20

NIVEAUX NGF

Repère	Altitude
Terrain / sol RDC	41,11 / 41,46
Arase fondations	39,02
Sous-face poutre-acrotère	44,08
Arase acrotère	44,75
Tête verrière	45,90

NOTES

1. Cotes en cm ; niveaux en m NGF (DOC-03 §1).
2. Poutre 8,03 m isostatique : 4 HA 14 + étriers HA 8 e = 300 ; contre-flèche de coffrage 20 mm.
3. Poutre perpendiculaire : 2 HA 12 + étriers HA 8 ; console de 0,70 m reprise par la nappe supérieure.
4. Poteau 25 × 25 : 6 HA 8, cadres HA 8 e = 200.
5. Voile de rive À CRÉER : 4 HA 12 par face + HA 8 e = 250, sur semelle filante 65 × 30 à NGF 39,02.
6. Joint de dilatation 20 mm entre extension et façade.

BET STRUCTURE — DOSSIER D'EXÉCUTION	**PL-02**
	Tâche 3 — plans généraux
Affaire GA-2026-58AIGLE — BET Structure 58 rue de l'Aigle — 92250 La Garenne-Colombes	Échelle : 1/50 A3 paysage
PL-02 — PLAN DE COFFRAGE DE L'EXTENSION	Indice B — 11/11/2026
Voile de rive sur semelle filante, poutre-acrotère isostatique, console et poteau BA	Échelle 1/50