PL-03 — COUPES ET ÉLÉVATIONS DE L'EXTENSION

Coupe transversale A-A, élévation du bord gauche et coupe sur le voile de rive

A — COUPE TRANSVERSALE A-A — 1/50

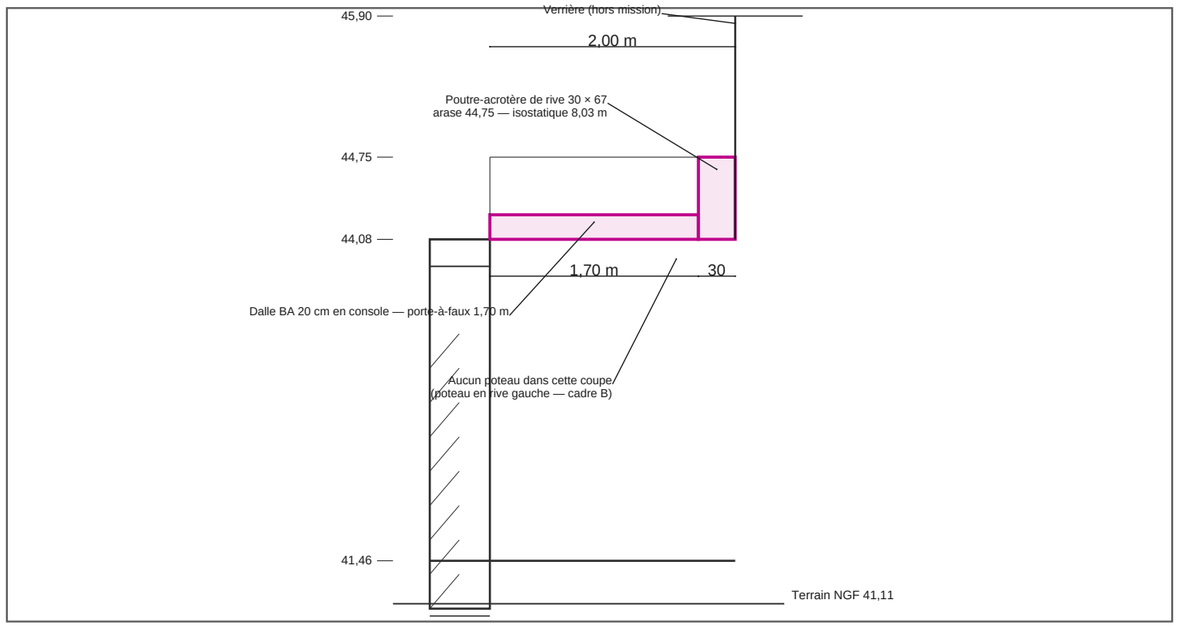

B — BORD GAUCHE : POTEAU ET CONSOLE — 1/40

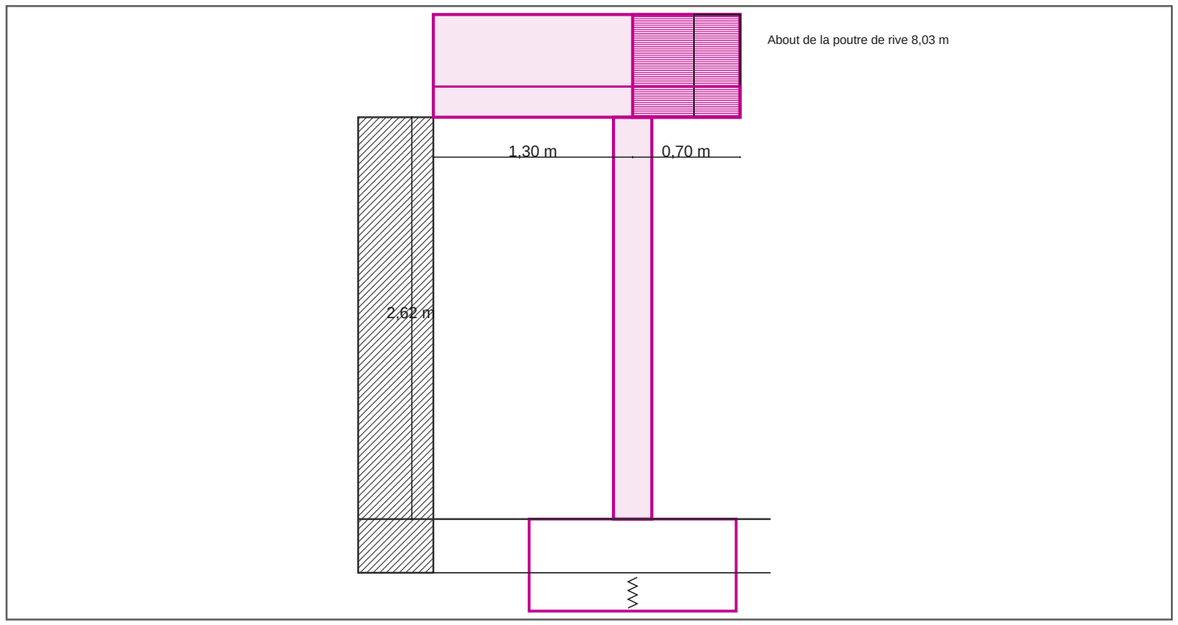

C — VOILE DE RIVE ET SEMELLE — 1/60

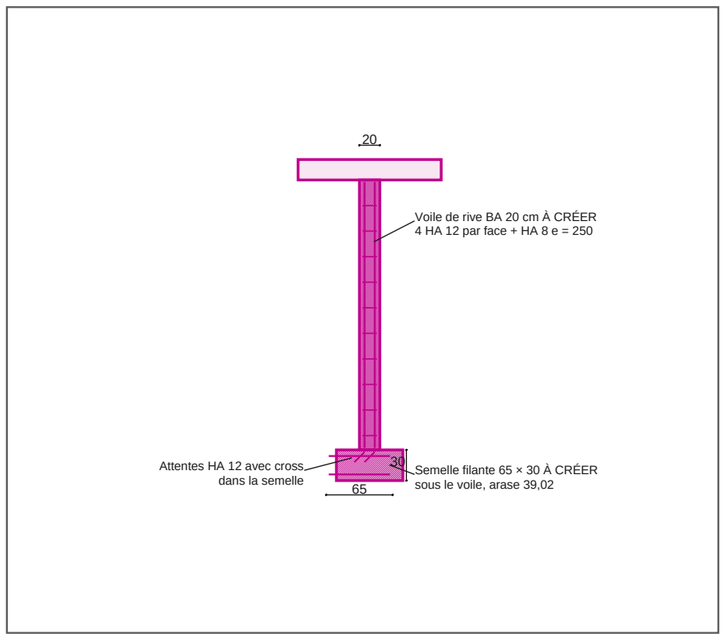

LÉGENDE

- Béton armé à créer
- Armatures B500B
- Maçonnerie existante

NOTES

1. Niveaux en m NGF ; sol fini RDC = 41,46 (DOC-01 §5).
2. Poutre-acrotère isostatique 8,03 m, arase 44,75, sous-face 44,08.
3. La dalle porte en console de 1,70 m depuis la façade.
4. Poteau BA 25 × 25 à 1,30 m du nu de façade (arbitrage E-02).
5. Puits de gros béton sous poteau : Ø 1,35 m, prof. 2,40 m, arase 39,02.
6. Voile de rive À CRÉER sur semelle filante 65 × 30, arase 39,02.
7. Contre-flèche de coffrage 20 mm sur la poutre de 8,03 m.

BET STRUCTURE — DOSSIER D'EXÉCUTION	**PL-03**
	Tâche 3 — plans généraux
Affaire GA-2026-58AIGLE — BET Structure 58 rue de l'Aigle — 92250 La Garenne-Colombes	Échelle : 1/50 A3 paysage
PL-03 — COUPES ET ÉLÉVATIONS	Indice A — 11/11/2026
Coupe transversale, élévation du poteau / console et coupe du voile neuf	Échelles : 1/40, 1/50 et 1/60