
# CROISSY-FLORA — B-25 (Ind. C) — CONTREVENTEMENT, TORSION ET JOINTS — STABILITÉ EN SERVICE
# PRINCIPE — NE PAS EXÉCUTER — Indice P  (ni vérification sismique D-26, ni stabilité provisoire D-27)

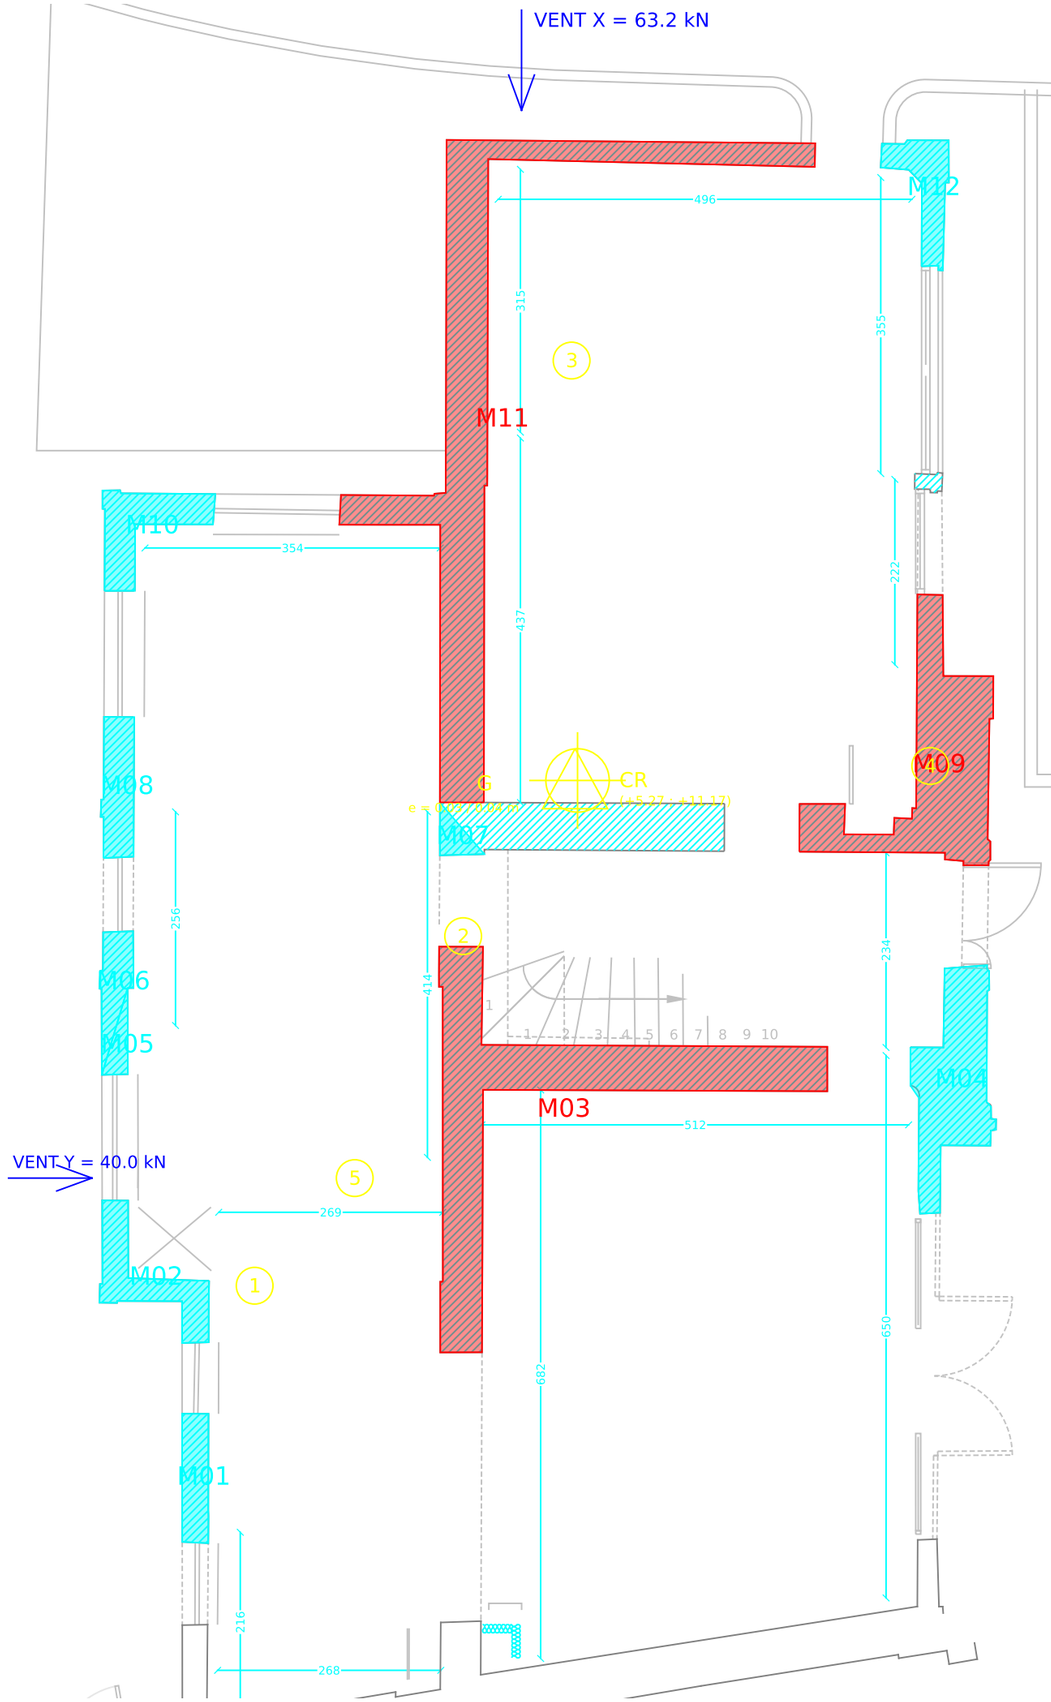


PRINCIPE — NE PAS EXECUTER — Indice P  (B-25 Ind. C)

## 1. SYSTEME DE CONTREVENTEMENT — VERDICT

La maçonnerie porteuse existante, et elle seule.
12 voiles comptes au RDC · 9 au R+1 · ΣKx = 1,21 GN/m · ΣKy = 1,64 GN/m
EXCLUS : frangements F1a/b/c, F2, F3, F4 · renforts R1/R2/R3/Stab1
poteaux P1-N/S, P2, P3, J1 · charpente · planchers (diaphragme flexible)
cloisons / doublages / isolants (V9 : jamais sur une vue structurelle)

## 2. VOILES COMPTES AU RDC — RAIDEURS HORIZONTALES

| ID | A(m²) | L(m) | t_eq(m) | Kx(kN/m) | Ky(kN/m) |
|---|---|---|---|---|---|
| M01 | 0.49 | 1.57 | 0.31 | 662 | 13521 |
| M02 | 0.80 | 2.04 | 0.39 | 21180 | 20005 |
| M03 * | 4.58 | 5.19 | 0.88 | 525216 | 439310 |
| M04 | 1.76 | 3.06 | 0.57 | 17609 | 100161 |
| M05 | 0.16 | 1.08 | 0.15 | 144 | 1518 |
| M06 | 0.42 | 1.76 | 0.24 | 771 | 9426 |
| M07 | 0.17 | 0.81 | 0.21 | 438 | 604 |
| M08 | 0.62 | 1.71 | 0.36 | 1139 | 19627 |
| M09 * | 2.79 | 3.28 | 0.85 | 113878 | 192477 |
| M10 | 0.79 | 1.65 | 0.48 | 16859 | 12758 |
| M11 * | 5.49 | 9.07 | 0.60 | 503490 | 815171 |
| M12 | 0.60 | 1.65 | 0.37 | 3620 | 16653 |

* voile majeur (M03 + M11 = 86 % de la raideur RDC)

## REPERES DE LA PLANCHE

1 R-1 : F2 + F3 supprimes -> fonction horizontale perdue, non reconstituee
2 R-2 : F1a perce le refend 50 cm -> voile scinde en 2 trumeaux
3 M11 voile majeur RDC (815 171 kN/m en Y) — grandeur transmise a la MOE
4 M09 voile majeur RDC cote Est (192 477 kN/m en Y) — idem M03
5 CR / G du RDC — ecart e_struct = 0,04 m (X) / 0,03 m (Y)

## 3. TORSION ET VERIFICATION SOUS VENT (EC1 / EC6)

G = (+5.24 ; +11.13) m  ·  CR = (+5.27 ; +11.17) m
e_struct : 0.04 m (vent X) · 0.03 m (vent Y)
e_accidentelle = ± 0,05 L = ± 0,87 m (X) · ± 0,55 m (Y)  → elle gouverne
Mt = 28.6 kN·m (X) · 11.6 kN·m (Y)
fvk = (0,15 + 0,4 x 0,30) / 2,5 = 108 kPa
tau/fvk max = 0.028  →  CAPACITE LARGEMENT TENUE

## 4. JOINTS DE DILATATION — AUCUN JOINT

Emprise 11,1 x 17,5 m · dilatation libre 5,2 mm · maçonnerie stabilisee
Frangements appuyes (portee <= 4,88 m) : aucune reprise de dilatation
-> D-28 consignee le 20/10/2026 : aucun joint · a reexaminer si l'emprise est modifiee

## 5. PHASE PROVISOIRE — HORS MISSION (D-27)

La verification du contreventement en phase provisoire incombe a la
maitrise d'oeuvre structure de conception (batiment existant).
AUCUNE verification provisoire n'est produite par nos soins.
Grandeurs transmises a la MOE (T-04) :
R+1  4 voiles majeurs = 88.9 % de la raideur totale
M08, M03, M09, M02
RDC  4 voiles majeurs = 95.1 % de la raideur totale
M11, M03, M09, M04
Restent de notre lot : etaiement d'execution (H-20) · mode operatoire
de pose · ordre F3 avant F2 · etaiement lateral des pignons (securite)

## 6. POSITION SISMIQUE — NON VERIFIEE (D-26)

Zone 1 (Ile-de-France) · seisme tres faible.
Arrete du 22/10/2010, art. 3 : aucune categorie d'importance n'est
soumise aux regles EC8 en zone 1 -> EC8 NON APPLICABLE.
DECISION CLIENT : aucune verification sismique produite, ni reglementaire,
ni de sensibilite. H-24 (sol C, agr 0,40) est neutralisee, non supprimee.

## 7. POINTS D'ARRET OUVERTS

PA-01 reconnaissance contradictoire de la continuite des voiles
M11/M03/M04 · M08/M03/M09 · trumeau M05 — AVANT TOUTE DEMOLITION
PA-02 verification de la liaison charpente-maconnerie des pignons — AVANT DEPOSE

PRESCRIPTION OBLIGATOIRE D-09 (REPRODUCTION INTEGRALE) :
« AU MEME NIVEAU QUE LES FONDATIONS EXISTANTES... RAJOUTER DU GROS BETON...
CETTE NOTE EST A INDIQUER SUR LES PLANS ET NOTE DE CALCULS »
0,00 RELATIF = plancher bas du RDC (D-20/D-21) · arase -1,00 m/TN mini (D-08/D-12) · 60x60 mini (D-14) · SF1 80x80 (D-30)

EHPAD LA ROSERAIE — PAVILLON FLORA (CROISSY-SUR-SEINE)

SCHEMA DE CONTREVENTEMENT — STABILITE GLOBALE (PH RDC)

Brique B-25 · Indice C · 20/10/2026 · Mode HYPOTHESE-NOTIFIEE · Regime OUTILLE (V13)

Fond B-32 Ind. D · Echelle 1/80 · Unites DXF cm · Repere B-30 (P1)

PRINCIPE — NE PAS EXECUTER — Indice P