PL-05/1 — ASSEMBLAGES ACIER / BA — REPRISES EN SOUS-ŒUVRE

Appuis de profilés S355 sur jambages et sommiers BA, encastrement en meulière, jonction sur poteau — 1/10

A — APPUI SUR JAMBAGE BA — 1/10

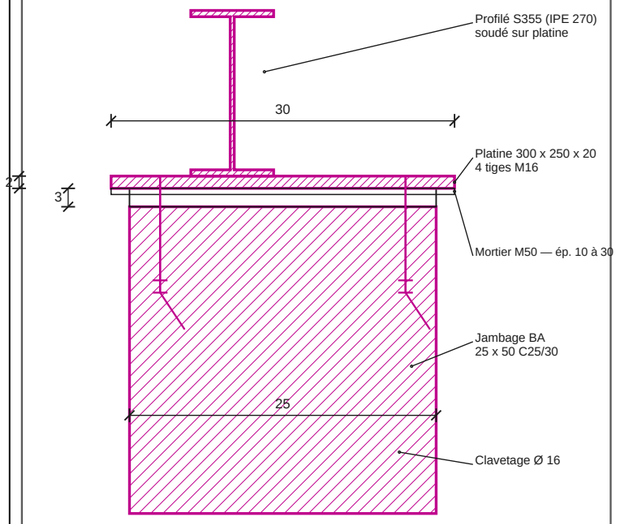

B — SOMMIER SOUS MUR — 1/10

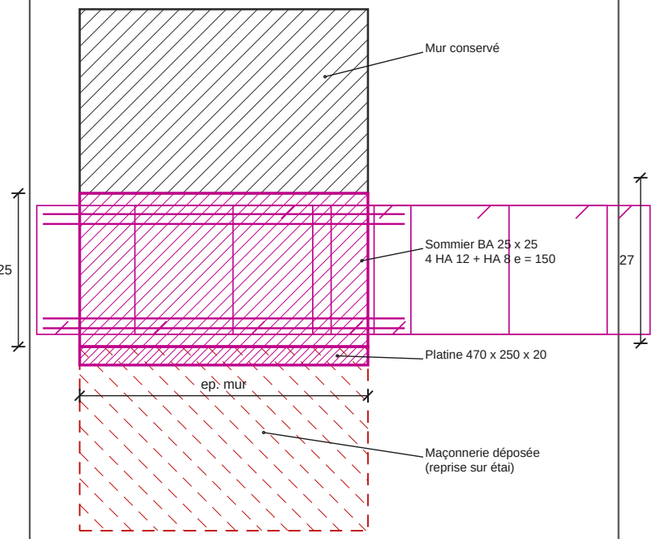

C — ENCASTREMENT MEULIÈRE — 1/10

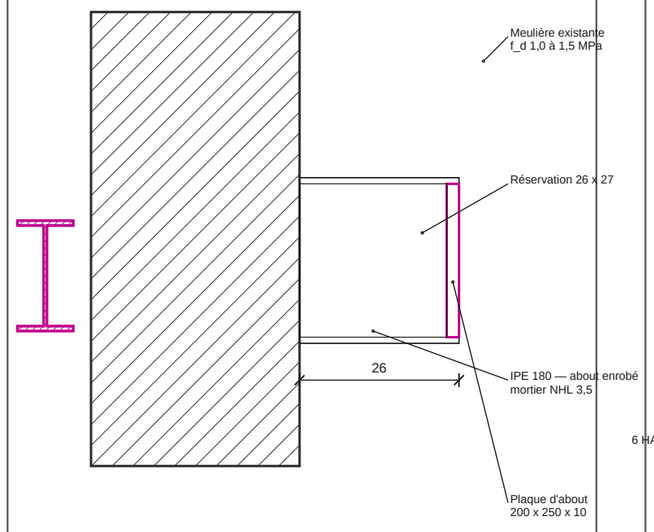

D — JONCTION SUR POTEAU — 1/14

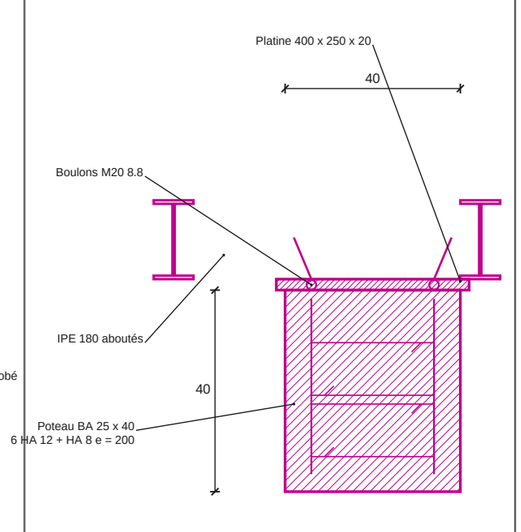

TABLEAU DES ASSEMBLAGES — PL-05/1

Rep.	Assemblage	Disposition	Reprise
A	Profilé / jambage BA	Platine + 4 tiges M16	M 44 kN·m
B	Profilé / sommier BA	Platine 470 x 250 x 20	V 87 kN
C	Profilé / meulière	Réservation 32 x 27	V 47 kN
D	Profilé / poteau BA	Platine + 4 M20 8.8	M 156 kN·m

DISPOSITIONS CONSTRUCTIVES

1. Platines et goussets soudés en atelier ; soudure d'atelier contrôlée 100 %.
2. Mortier de calage sans retrait classe M50, épaisseur 10 à 30 mm.
3. Tiges d'ancrage : perçage Ø 18, résine chimique, profondeur 15 cm mini.
4. Clavetage dans la meulière : scellement à la résine après dépoussiérage et humidification.
5. Toutes les platines en contact avec la maçonnerie reçoivent une protection anticorrosion.
6. Reprise provisoire sur étais métalliques avant dépose de toute maçonnerie porteuse.

TOLÉRANCES

1. Implantation ± 10 mm.
2. Niveau d'assise ± 5 mm.
3. Verticalité du poteau : H/500.
4. Serrage boulons au couple prescrit.

BET STRUCTURE — DOSSIER D'EXÉCUTION	**PL-05/1**
	Tâche 4 — détails d'exécution
Affaire GA-2026-58AIGLE — BET Structure 58 rue de l'Aigle — 92250 La Garenne-Colombes	Échelle : 1/10 A3 paysage
PL-05/1 — ASSEMBLAGES RSO ACIER / BA	Indice A — 11/11/2026
Appuis de profilés S355 sur jambages et sommiers BA	S355 — C25/30

PL-05/2 — ASSEMBLAGES ACIER / BA — EXTENSION

Appui glissant de la poutre-acrotère sur le voile, appui sur poteau, ancrage de la dalle — 1/10

E — APPUI GLISSANT VOILE — 1/10

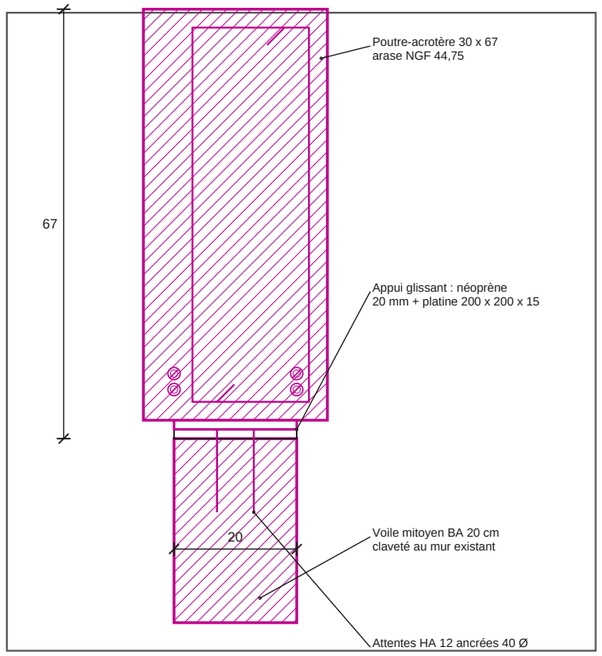

F — APPUI SUR POTEAU BA — 1/10

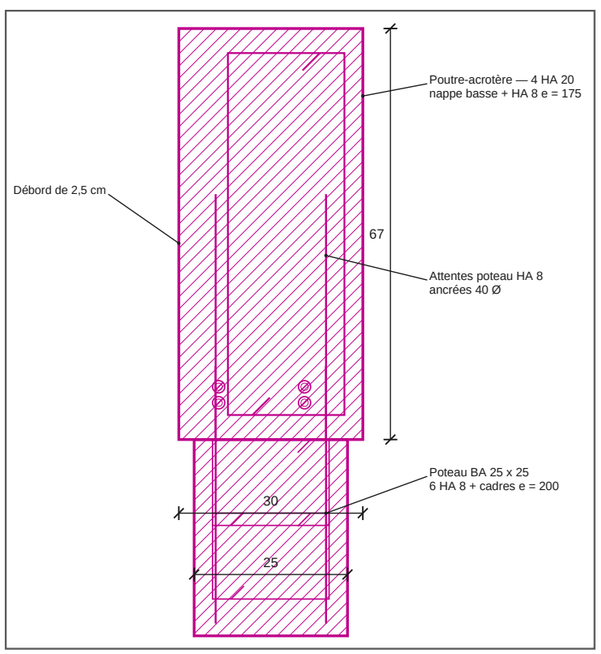

G — ANCRAGE DALLE FAÇADE — 1/10

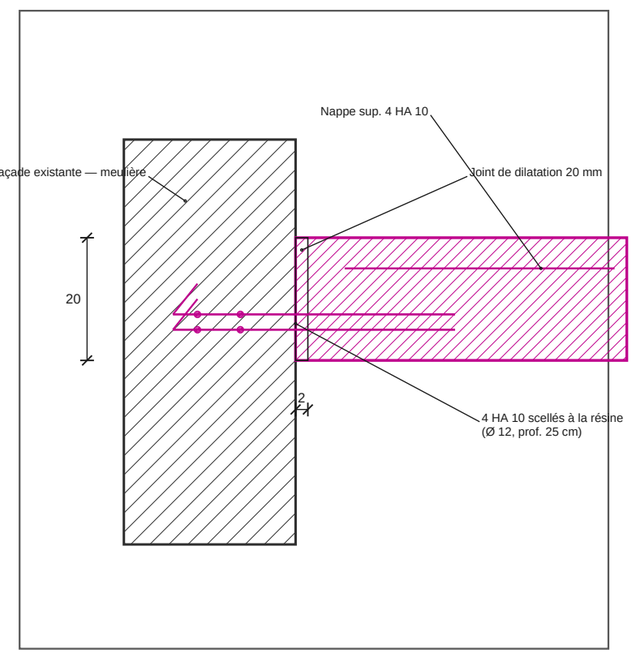

H — CLAVETAGE VOILE — 1/10

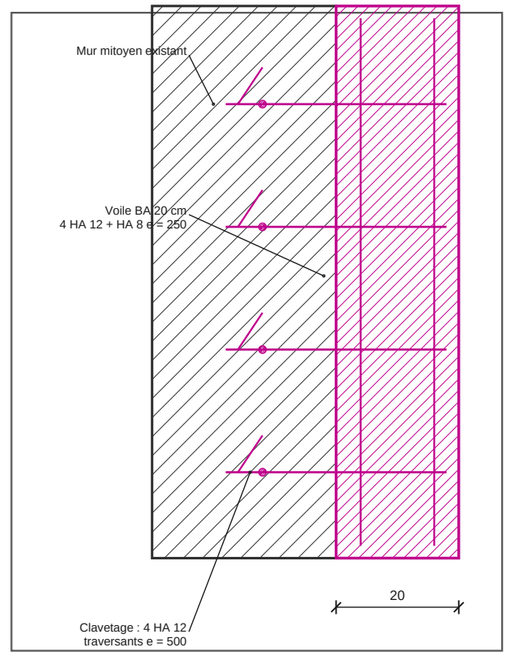

TABLEAU DES ASSEMBLAGES — PL-05/2

Rep.	Assemblage	Disposition	Reprise
E	Poutre-acrotère / voile	Néoprène 20 mm + platine	V 130,8 kN
F	Poutre-acrotère / poteau	Attentes HA 8 (40 Ø)	N 137,5 kN
G	Dalle / façade	4 HA 10 scellés résine	M 9,1 kN·m/m
H	Voile / mur mitoyen	4 HA 12 traversants	p 32,9 kN/m²

NOTES DE MISE EN ŒUVRE

1. Appui glissant de la poutre-acrotère : néoprène 200 x 200 x 20 mm, un par appui.
2. Le poteau BA à 2,00 m est l'appui fixe ; le voile mitoyen est l'appui glissant (libre dilatation).
3. Attentes HA 8 du poteau : longueur d'ancrage 40 Ø = 80 cm dans la poutre.
4. Scellements résine : Ø de perçage = Ø barre + 4 mm ; profondeur 25 cm ; ancrage en traction à contrôler.
5. Joint de dilatation 20 mm entre dalle terrasse et façade : fond de joint + mastic élastomère.
6. Aucune soudure sur site sur les profilés principaux sans accord écrit du BET.

PHASAGE

1. Étaiement.
2. Démolition.
3. Jambages.
4. Pose profilés.
5. Clavetage.
6. Dépose étais.

BET STRUCTURE — DOSSIER D'EXÉCUTION	**PL-05/2**
	Tâche 4 — détails d'exécution
Affaire GA-2026-58AIGLE — BET Structure 58 rue de l'Aigle — 92250 La Garenne-Colombes	Échelle : 1/10 A3 paysage
PL-05/2 — ASSEMBLAGES EXTENSION	Indice A — 11/11/2026
Appuis de la poutre-acrotère et ancrages de la dalle	C25/30 — B500B