
CROISSY-FLORA — PLS (D-11) / B-20 Ind. B & B-40 Ind. E — IMPLANTATION DES FONDATIONS SUR VUE EN PLAN NETTOYÉE
PRINCIPE — NE PAS EXÉCUTER — Indice P (Semelle SF1 60×60 mini + Bêche BA + Nuages D-19 sur appuis P1/P3/J1)

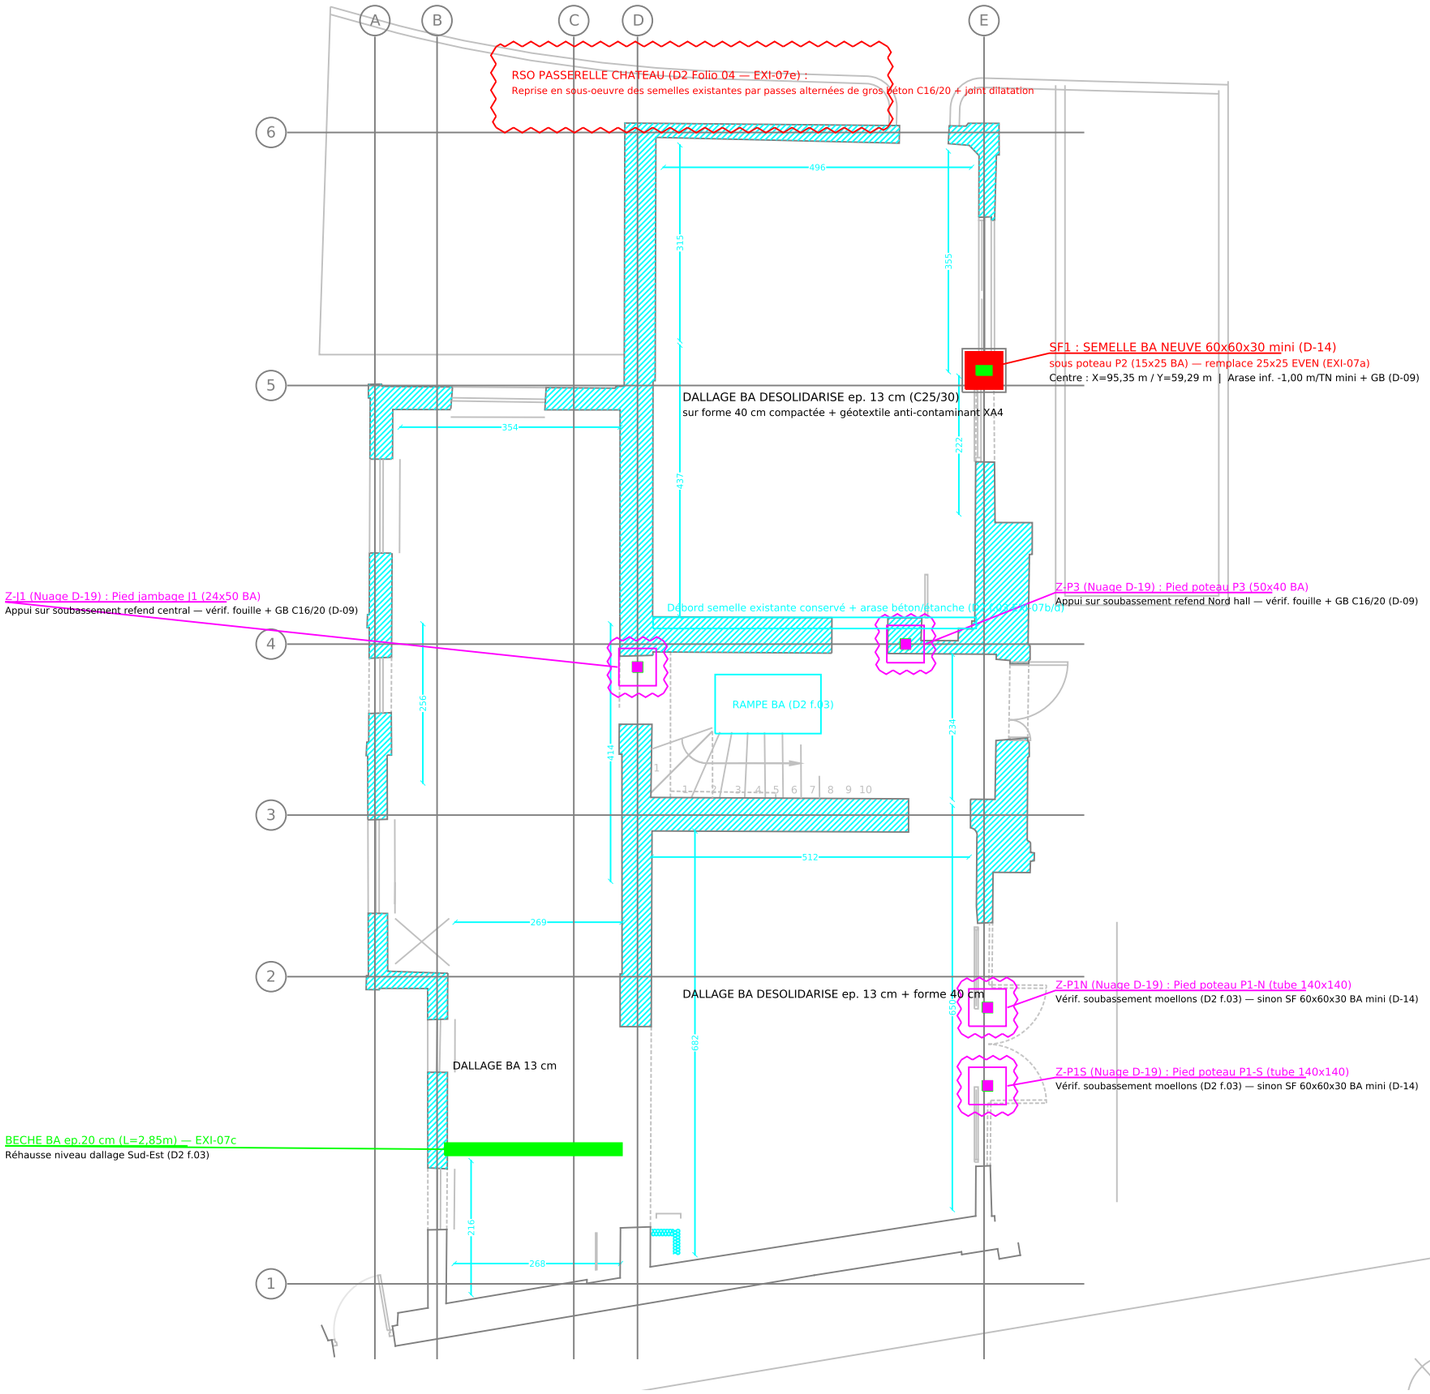

PLS — PLAN D'IMPLANTATION DES FONDATIONS — PRINCIPE — NE PAS EXECUTER — Indice P


1. TABLEAU D'IMPLANTATION DES OUVRAGES D'INFRASTRUCTURE (REP. B-30 / D5)

OUVRAGE	NATURE & DIMENSIONS MINIMALES	COORD. DXF (m)	B-30 (m)	STATUT
SF1	Semelle isolée BA 60x60x30 mini (D-14)	X=95,35 Y=59,29	+9,48 / +14,87	CERTAIN (sous P2)
Z-P1N	Appui P1-N : vérif. moellons ou SF 60x60	X=95,41 Y=49,04	+9,54 / +4,62	NUAGE D-19
Z-P1S	Appui P1-S : vérif. moellons ou SF 60x60	X=95,41 Y=47,78	+9,54 / +3,36	NUAGE D-19
Z-P3	Appui P3 (50x40 BA) sur soubassement	X=94,09 Y=54,89	+8,22 / +10,46	NUAGE D-19
Z-J1	Appui J1 (24x50 BA) sur soubassement	X=89,78 Y=54,52	+3,91 / +10,09	NUAGE D-19
BECHE	Bêche BA ep. 20 cm, L = 2,85 m (EXI-07c)	X=86,67->89,53	Y = 46,77 m	CONTRACTUEL D2
RSO-PASS	Passes alternées gros béton C16/20	X=87,7 ->93,5	Y = 63,3..64,3m	CONTRACTUEL D2
DALLAGE	BA ep. 13 cm désolidarisé + forme 40 cm	Zones Nord, Sud et Sud-Est		CONTRACTUEL D1/D2

NOTE OBLIGATOIRE D-09 (TEXTE INTEGRAL) & PRESCRIPTION D'EXECUTION ENC v3 :
« AU MEME NIVEAU QUE LES FONDATIONS EXISTANTES... RAJOUTER DU GROS BETON...
CETTE NOTE EST A INDIQUER SUR LES PLANS ET NOTE DE CALCULS »

1. Arase inférieure des fondations neuves : -1,00 m / TN MINIMUM (jamais remontée — D-08 / D-12).
2. Encastrement minimal dans les alluvions anciennes : 0,50 m ; q_ELS <= 0,30 MPa, q_ELU <= 0,49 MPa.
3. Dimension minimale absolue : 60 x 60 cm (D-14) — capacité 60x60 : 108 kN ELS / 176,4 kN ELU.
   Ferraillage type B-40 : HA8 e150 inf. dans les 2 sens (335 mm²/m >= A_s,min), c_nom = 50 mm.
4. Vérification systématique à l'ouverture des fouilles du niveau des fondations existantes adjacentes :
   - si l'existant est PLUS PROFOND : descendre à son niveau et rattraper en GROS BETON C16/20 sous semelle ;
   - si l'existant est MOINS PROFOND : maintenir -1,00 m / TN minimum sans déchausser l'existant.
5. Interdiction absolue de déchausser les soubassements en moellons ; passes alternées <= 1,00 m (H-13).
6. Fouilles réputées hors nappe (D-16) : toute venue d'eau = POINT D'ARRET et constat contradictoire.
7. Tassements hors mission GO (D-15, charge géotechnicien). Réception de fond de fouille obligatoire.

2. COUPE DE PRINCIPE FONDATION NEUVE SF1 + GROS BETON (D-08 / D-09 / D-14)

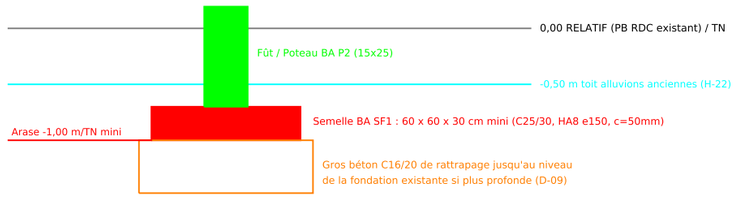

EHPAD LA ROSERAIE — PAVILLON FLORA (CROISSY-SUR-SEINE)

PLS (D-11) — IMPLANTATION DES FONDATIONS & INFRASTRUCTURE PB RDC (SANS CLOISONS NI ISOLATION)

Briques B-20 Ind. B / B-40 Ind. E · 20/10/2026 · Support de travail & validation client (Nuages D-19)

Semelle SF1 (60x60x30 mini D-14) + Bêche BA + RSO Passerelle + Points de vérification soubassements

PRINCIPE — NE PAS EXECUTER — Indice P

Echelle plan 1/80 · Unités DXF : cm · CARNAC v2.6 · Audit DXF : 0 erreur