
EHPAD LA ROSERAIE — PAVILLON FLORA — CROISSY-SUR-SEINE

PLAN D'EXÉCUTION — CHARPENTE BOIS NEUVE — Ind. B — 21/10/2026

C24 · service 2 · demi-fermes désolidarisées du plancher · E-07 non chargé

NE PAS EXÉCUTER SANS VISA


Protection au feu adéquate à prévoir (hors lot GO)

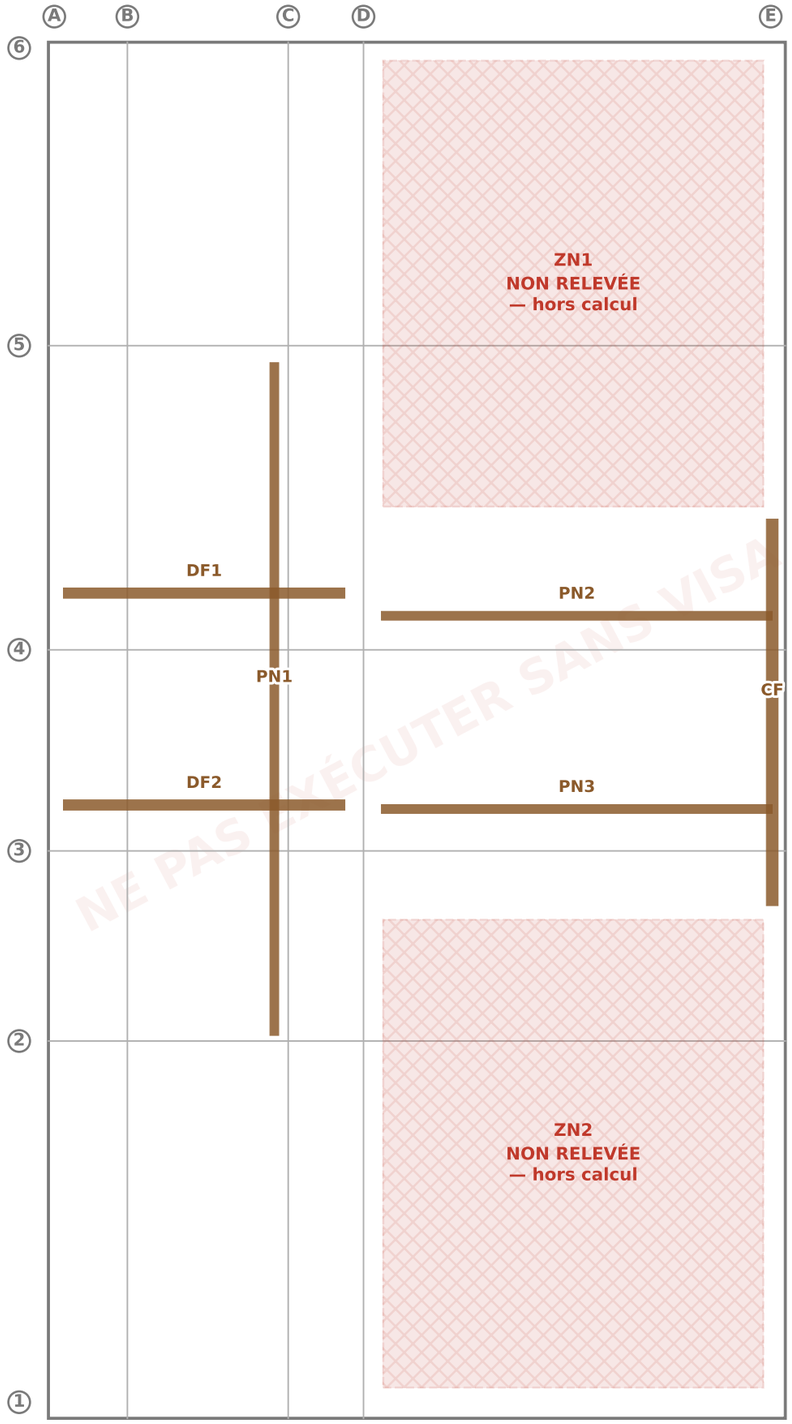

EXISTANT — trait gris · NEUF — couleur

Demi-ferme · schéma · C24

Appuis murs Files A et C — pas le plancher

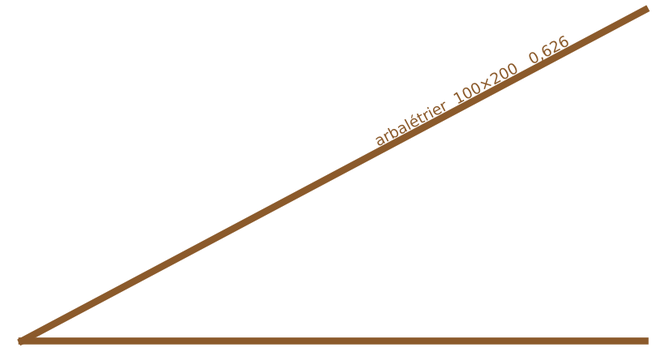

Nomenclature

Rep.	Section	L	Taux max
PN1/2/3	75×200 C24	3,20 m	0,830 (flèche)
DF-arb	100×200 C24	3,62 m	0,626
DF-ent	75×200 C24	3,20 m	0,108
CF	75×225 C24	2,62 m	0,940 (flambement)

Contreventement de toiture : absent au D2 — non inventé.

Sabots : non catalogués — non inventés.

ZN1 / ZN2 : relevé avant toute taille.

Échelle plan ~1/100 · Ind. B remplace Ind. A (présentation, aucun chiffre modifié)