
# EHPAD LA ROSERAIE — PAVILLON FLORA — CROISSY-SUR-SEINE

**NE PAS EXÉCUTER SANS VISA**

PLAN D'EXÉCUTION — FONDATIONS (RDC BAS) — Ind. B — 21/10/2026


Protection au feu adéquate à prévoir (hors lot GO)

C25/30 · S500B · arase inf. −1,00 m / TN mini · c_nom 50 mm · PARTIEL-DÉCLARÉ

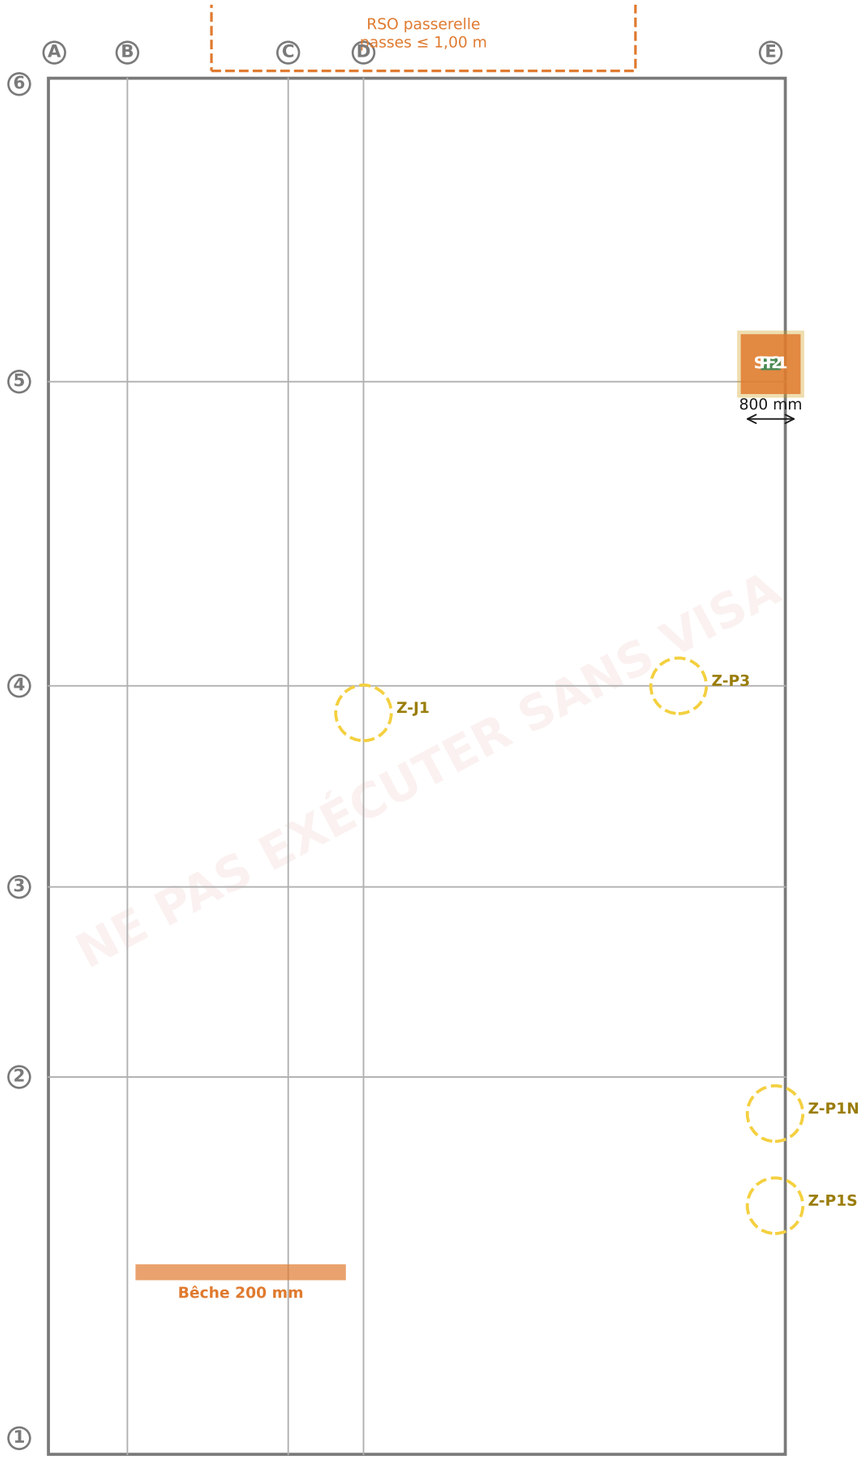


*EXISTANT — trait gris · NEUF — couleur*

Coupe A-A — SF1 800×800×250 · 1/20

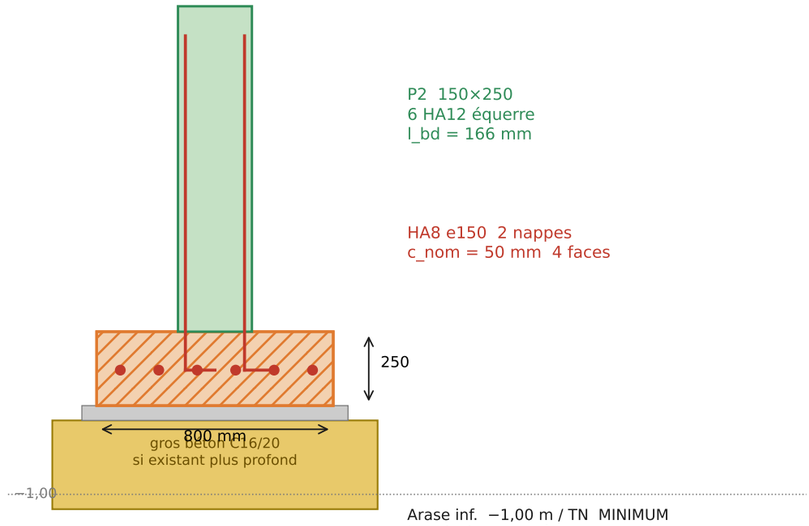


**Nomenclature — façonnage → B-62**

| Rep. | Ouvrage | Qté |
|---|---|---|
| SF1 | Semelle 800×800×250 C25/30 | 1 |
| HA8 | Lit inf. e150 6+6 | 1 nappe |
| HA12 | Attentes P2 équerre | 6 |
| GB | C16/20 sous semelle | selon fouille |
| BP | Propreté 50 mm | 1 |
| Bêche | 200 mm × 2,85 m | 1 |
| RSO | Passes ≤ 1,00 m C16/20 | 1 zone |
| Type | 600×600×300 si fouille | selon constat |

Fouille : réception contradictoire avant coulage.

Nuages jaunes = reconnaissance en fouille (ouverte).

NE PAS EXÉCUTER SANS VISA