
EHPAD LA ROSERAIE — PAVILLON FLORA — CROISSY-SUR-SEINE

PLAN D'EXÉCUTION — LINTEAUX — Ind. B — 21/10/2026

S275 · F1 = 2×HEA 200 · R3 = UPE 200 rempli C25/30


NE PAS EXÉCUTER SANS VISA

Protection au feu adéquate à prévoir (hors lot GO)

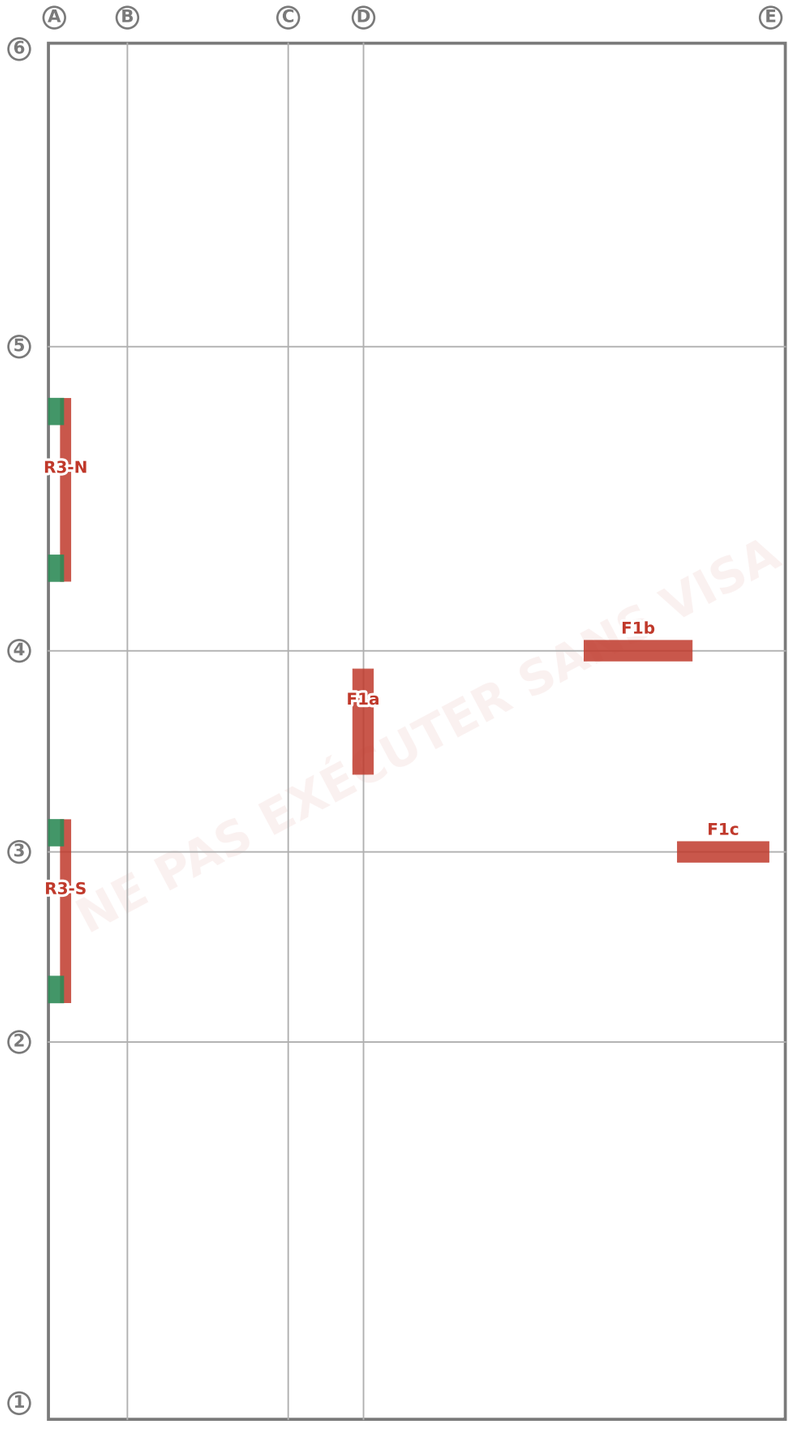

EXISTANT — trait gris · NEUF — couleur

Coupe R3 — UPE 200 + béton · 1/10

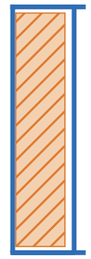

UPE 200
rempli C25/30
(sans béton : τ = 1,40)

L = 1,55 m · 2 appuis S1
E-08 bois court-circuité

Nomenclature

Rep.	Profil	L	Appuis
F1a	2×HEA 200	1,00 m	S2 + J1
F1b	2×HEA 200	0,90 m	S2 + P3
F1c	2×HEA 200	0,85 m	2×S2
R3-N	UPE 200 + B	1,55 m	2×S1
R3-S	UPE 200 + B	1,55 m	2×S1

Seuils BA : SANS OBJET.

Linteaux bois existants : hors lot (non prescrit).

S1 sur abouts de mur, hors bois.

NE PAS EXÉCUTER SANS VISA