
EHPAD LA ROSERAIE — PAVILLON FLORA — CROISSY-SUR-SEINE

PLAN D'EXÉCUTION — COUSSINS D'APPUI — Ind. B — 21/10/2026

C25/30 · w_b = 300 mm mini · 6 appuis sous R1 / F2 / F3

NE PAS EXÉCUTER SANS VISA


Protection au feu adéquate à prévoir (hors lot GO)

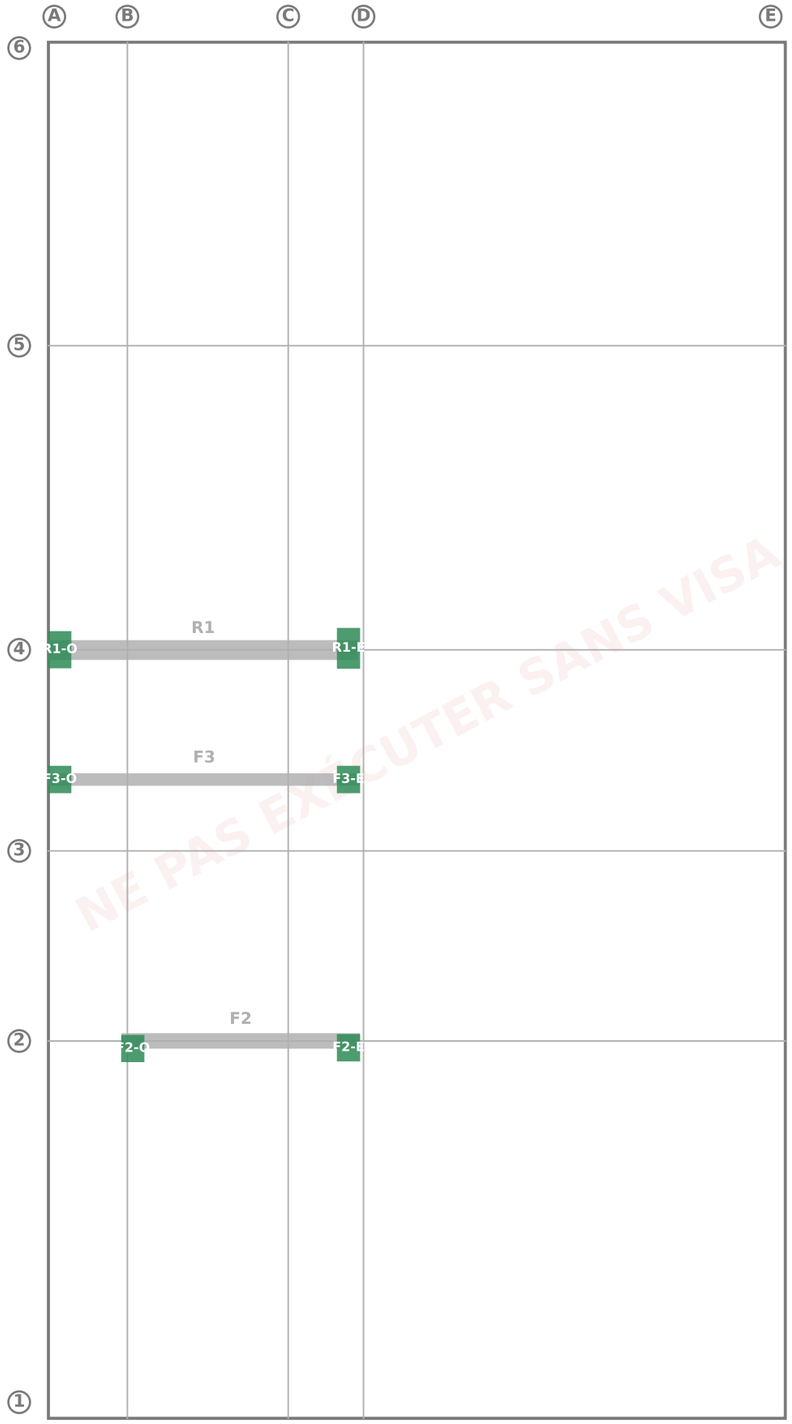

EXISTANT — trait gris · NEUF — couleur

Coussin type · 1/10

h = 200 mm C25/30
4 HA8
mortier complet
e ≤ t/4 du nu de mur

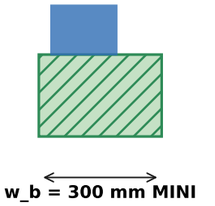

Nomenclature

Rep.	Sous	V_Ed	Section
C-R1-O/E	R1	77,4 kN	300×500×200
C-F2-O/E	F2	62,4 kN	300×400×200
C-F3-O/E	F3	61,6 kN	300×400×200

TOTAL 6 coussins. Ne pas réduire w_b.

F1 / R3 : S1 200 mm suffisent — pas de coussin.

R2 / F4 : OK sans coussin.

Ce ne sont PAS des linteaux.

NE PAS EXÉCUTER SANS VISA

Échelle plan ~1/100 · détail 1/10 · Ind. B remplace Ind. A (présentation, aucun chiffre modifié)