
EHPAD LA ROSERAIE — PAVILLON FLORA — CROISSY-SUR-SEINE

PLAN D'EXÉCUTION — STRUCTURE MÉTALLIQUE — Ind. B — 21/10/2026

S275 · F3 : aucune charge ajoutée (flèche 0,971 × L/300)

NE PAS EXÉCUTER SANS VISA

Protection au feu adéquate à prévoir (hors lot GO)

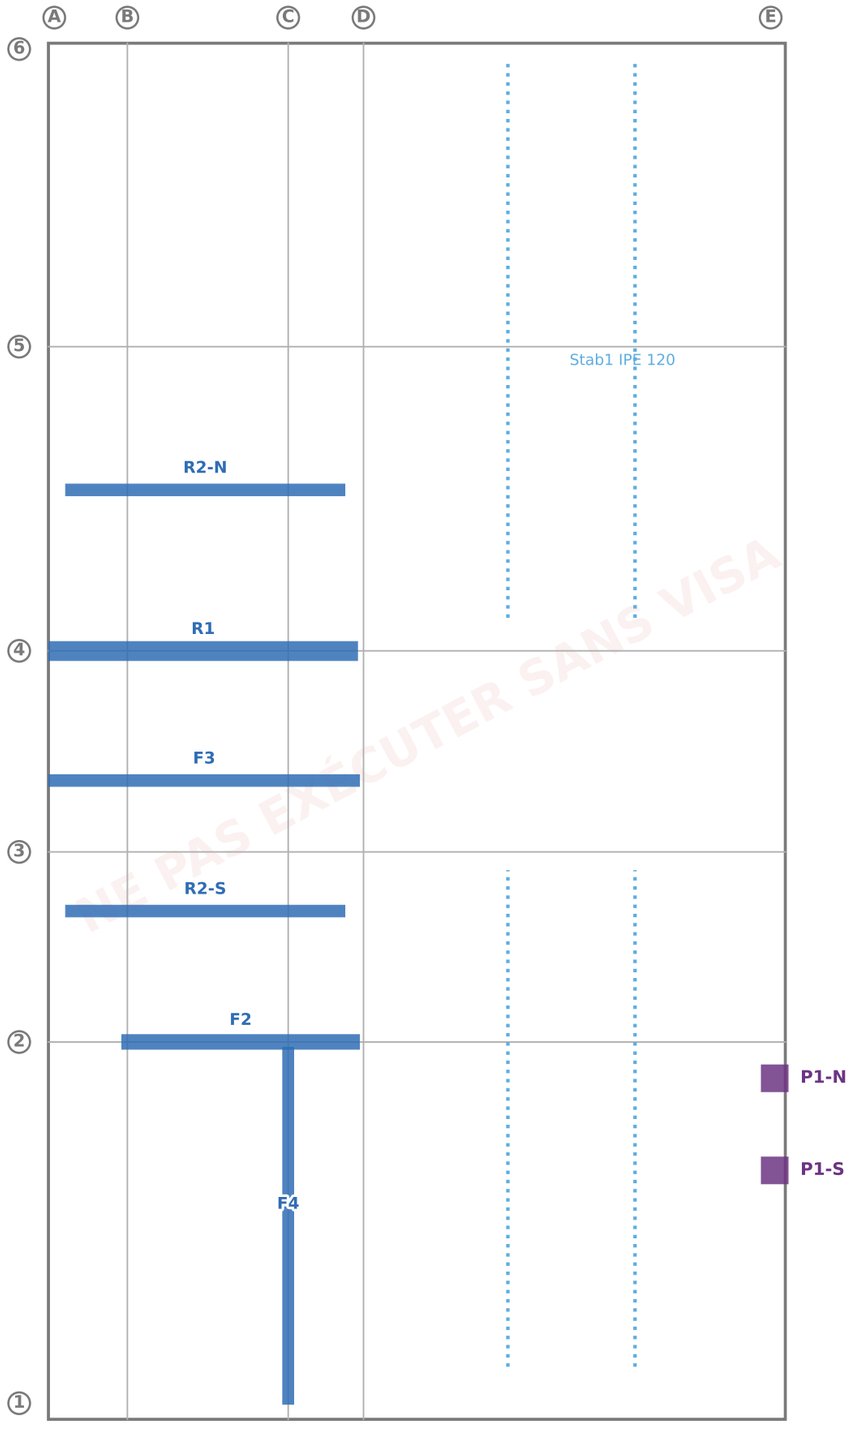

EXISTANT — trait gris · NEUF — couleur

Profilés — S275 — classe 1

F2 HEB 200 L=2,85 m M 0,252 w 0,237

F3 HEB 160 L=3,85 m M 0,609 w 0,971 ←

F4 IPE 200 L=4,88 m M 0,231 w 0,306

R1 2×UPE 200 L=3,85 m LT 0,880 w 0,927

R2 HEB 160 L=3,82 m ×2

P1 SHS 140×6,3 N_Ed 100,3 kN flamb. 0,123

Stab1 IPE 120 4 files 5,8 kN / file

F3 : 12,5 mm pour 12,8 mm admis.

Toute charge ajoutée (y c. C4) = non conforme.

IPE 330 existant : hors calcul.

R3 / F1 : voir LINTEAU. Coussins : MACON.

Nomenclature

Rep.	Profil	L (mm)	Qté
F2	HEB 200	2 850	1
F3	HEB 160	3 850	1
F4	IPE 200	4 880	1
R1	UPE 200	3 850	2
R2-N/S	HEB 160	3 820	2
P1-N/S	SHS 140×140×6,3	3 000	2
Stab1	IPE 120	selon relevé	4

Remplissage UPE R3 : C25/30 (METAL / LINTEAU).

NE PAS EXÉCUTER SANS VISA