
EHPAD LA ROSERAIE — PAVILLON FLORA — CROISSY-SUR-SEINE

NE PAS EXÉCUTER SANS VISA

PLAN D'EXÉCUTION — DALLAGE RDC BAS — Ind. B — 21/10/2026


Protection au feu adéquate à prévoir (hors lot GO)

C25/30 130 mm · ST25C · 111,15 m² · joints de retrait e ≤ 4,50 m

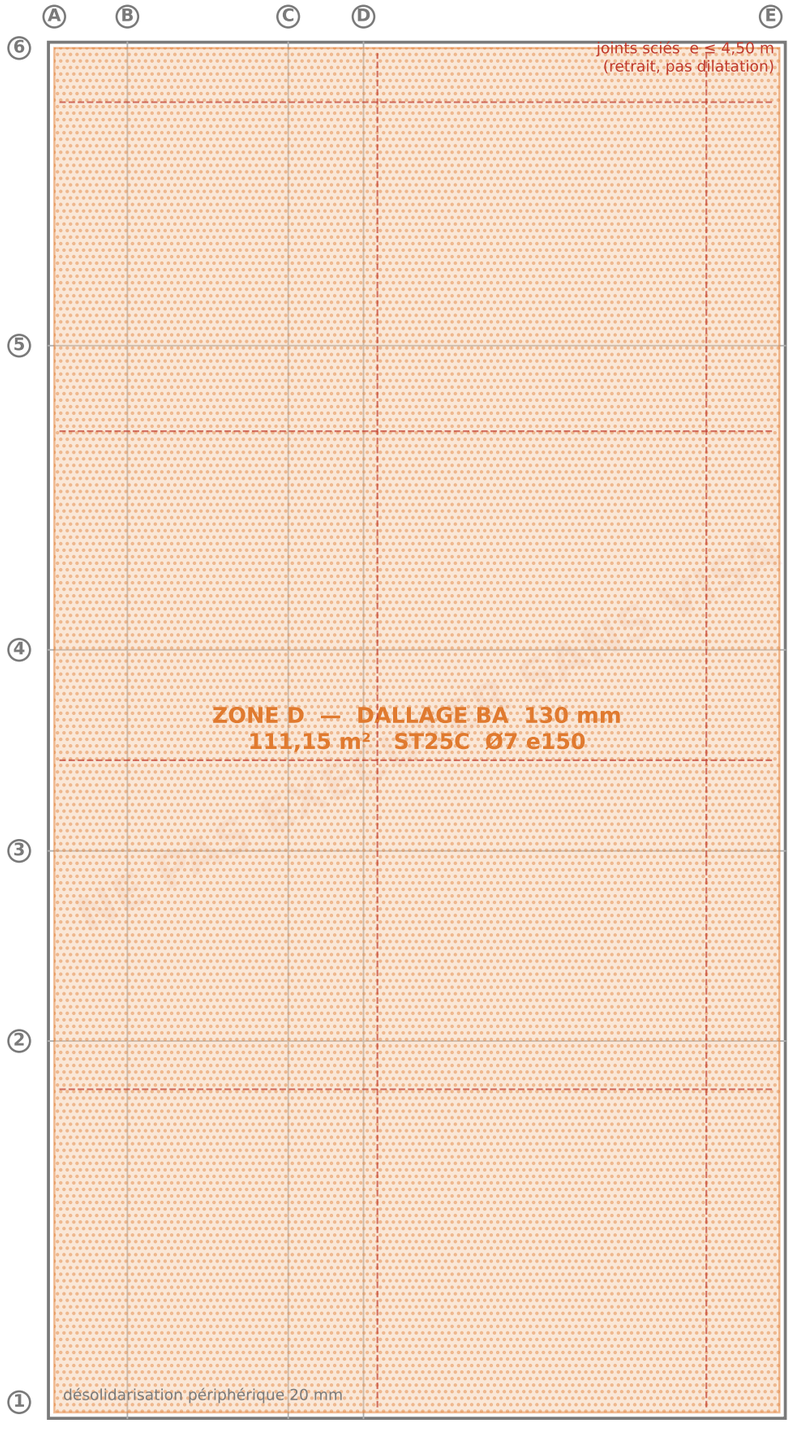

EXISTANT — trait gris · NEUF — couleur

Coupe type dallage · 1/10

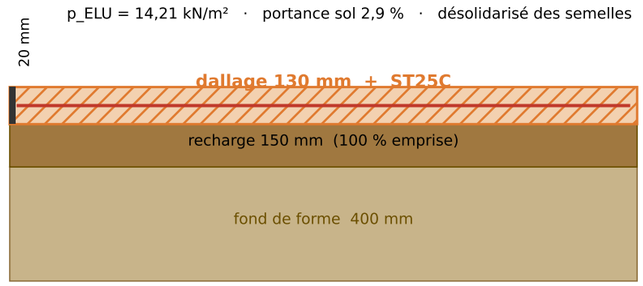

Nomenclature

Rep.	Ouvrage	Qté
Dallage	BA 130 mm C25/30 111,15 m²	1
ST25C	Ø7 e150 257 mm²/m 2 nappes	1
Joints	sciés e ≤ 4 500 mm	selon plan
Bandes	polystyrène 20 mm périphérie	1
Recharge	150 mm sous dallage	100 %

Zone A solives 8×18 : EXISTANT — hors ce plan.

Zone B IPE 160/330 : EXISTANT — voir métal.

Plancher haut E-07 : non sondé — non chargé.

Échelle plan ~1/100 · coupe 1/10 · Ind. B remplace Ind. A (présentation, aucun chiffre modifié)