
EHPAD LA ROSERAIE — PAVILLON FLORA — CROISSY-SUR-SEINE

PLAN D'EXÉCUTION — POTEAUX ET JAMBAGES BA — Ind. B — 21/10/2026

C25/30 · S500B · c_nom 30 mm · 6 HA12 partout · H = 2,80 m (à relever)


NE PAS EXÉCUTER SANS VISA

Protection au feu adéquate à prévoir (hors lot GO)

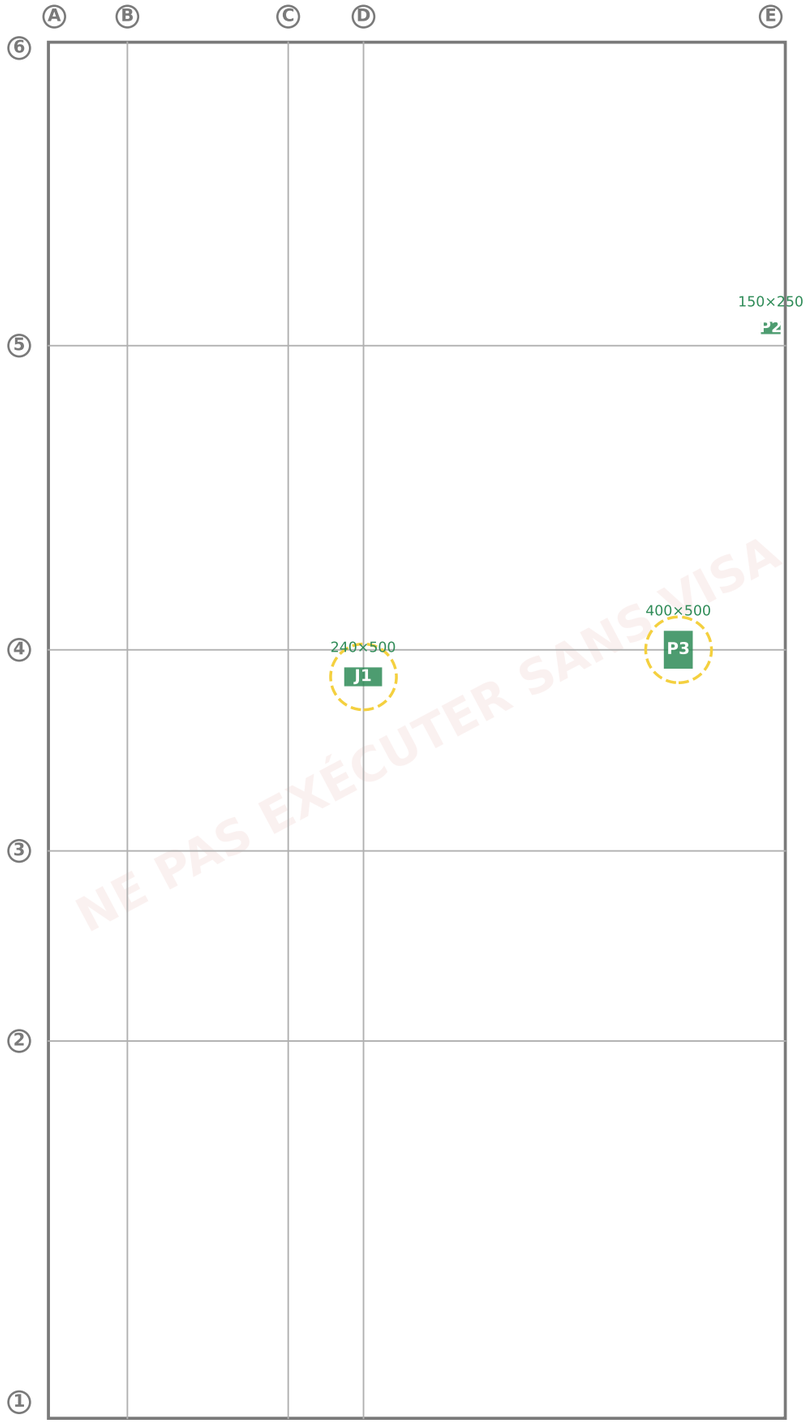

EXISTANT — trait gris · NEUF — couleur

Coupe type P2 150×250 · 1/20

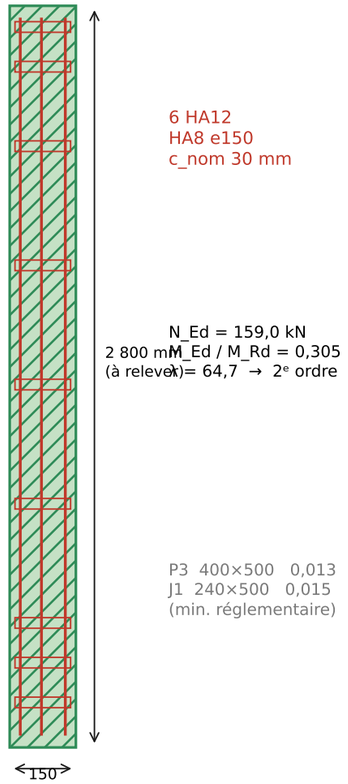

Nomenclature — façonnage → B-62

Rep.	Section mm	Acier	N_Ed	Taux
P2	150 × 250	6 HA12	159,0 kN	0,305
P3	400 × 500	6 HA12	35,8 kN	0,013
J1	240 × 500	6 HA12	39,8 kN	0,015

Cadres HA8 e150 (P2) / e200 (P3, J1)

6 HA12 imposé par l'espacement max., pas par As,min.

Appui J1 sur maçonnerie : 0,332 MPa (f_k = 1,5 MPa).

H = 2 800 mm = hypothèse — relevé avant façonnage.

NE PAS EXÉCUTER SANS VISA