

CROISSY-FLORA — B-60 Ind. A — VERTICAUX BA EXE COTÉS (P2 / P3 / J1)
NE PAS EXÉCUTER SANS EXE COTÉ ET VISA (Fond B-32 Ind. D : cloisons et isolation supprimées)

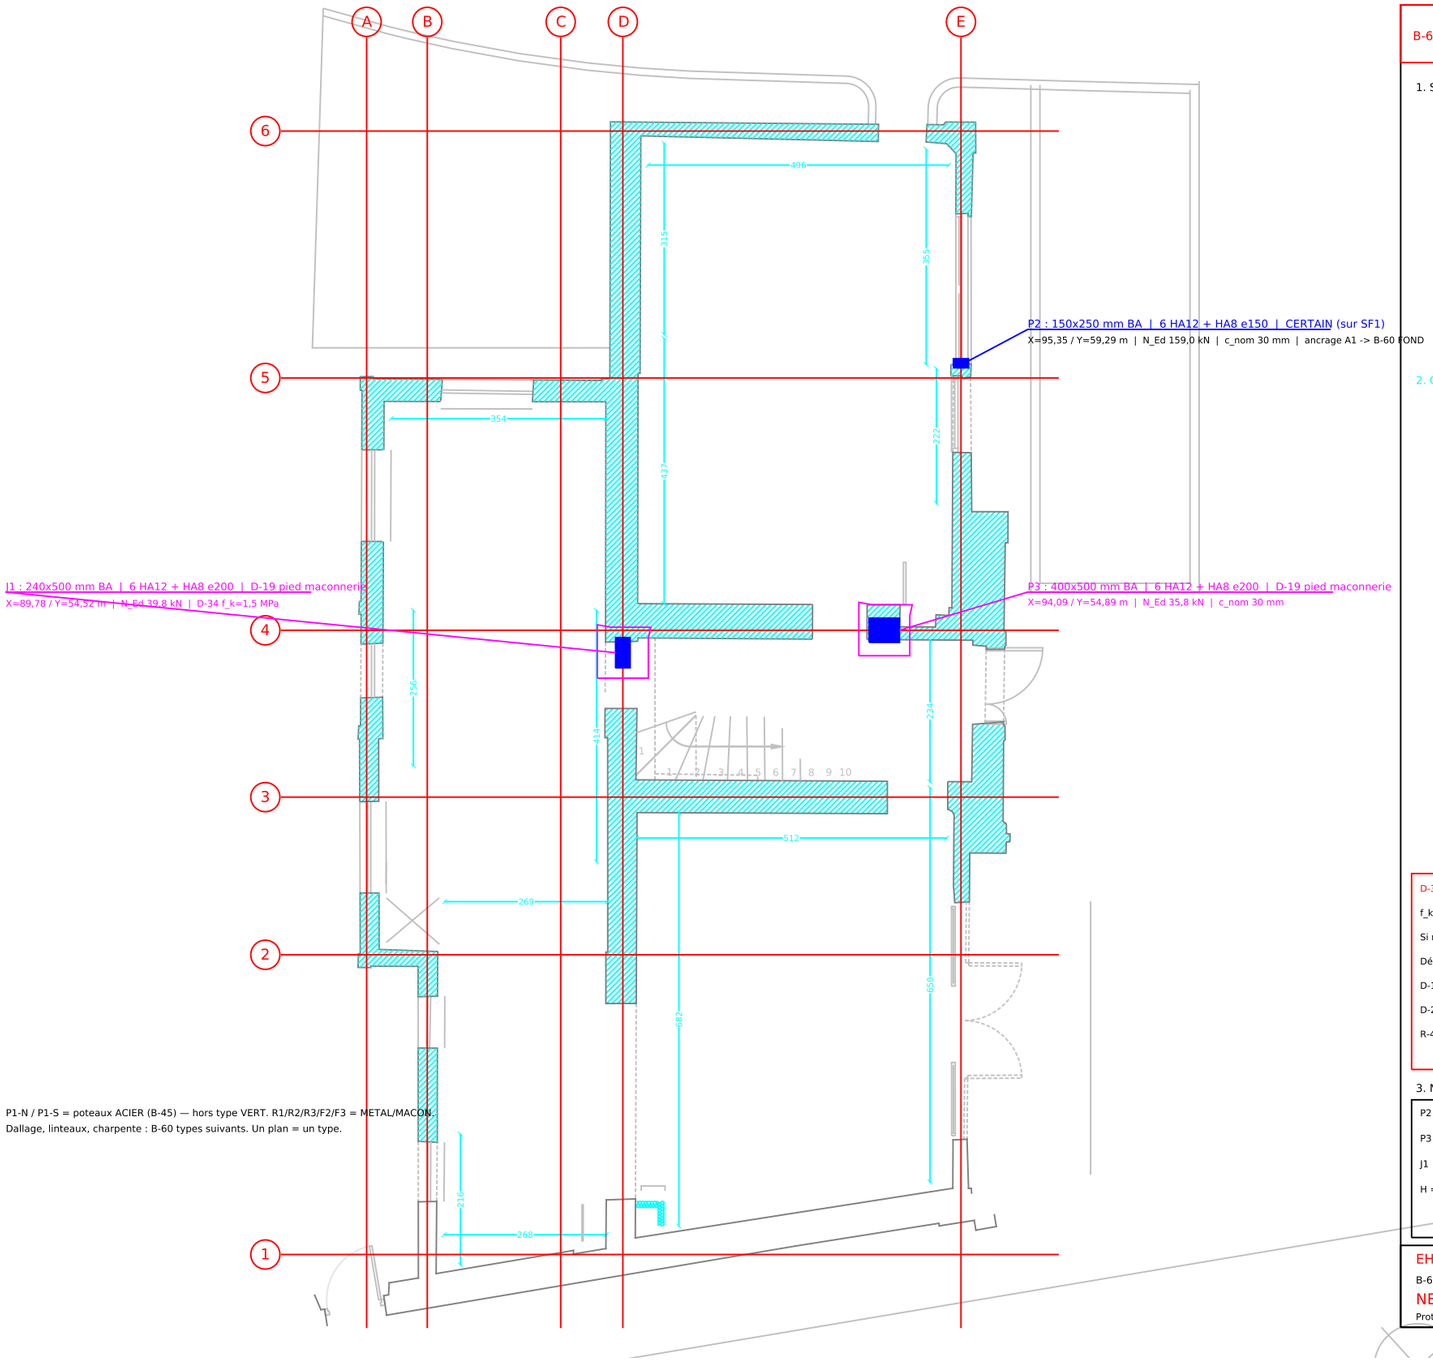


P1-N / P1-S = poteaux ACIER (B-45) — hors type VERT. R1/R2/R3/F2/F3 = METAL/MACON.
Dallage, linteaux, charpente : B-60 types suivants. Un plan = un type.

B-60 Ind. A | VERT EXE | P2 / P3 / J1 | NE PAS EXECUTER SANS EXE COTE ET VISA (PARTIEL-DECLARE)

1. SECTIONS COFFRAGE + FERRAILLAGE — 6 HA12 S500B — c_nom = 30 mm — cotes en mm

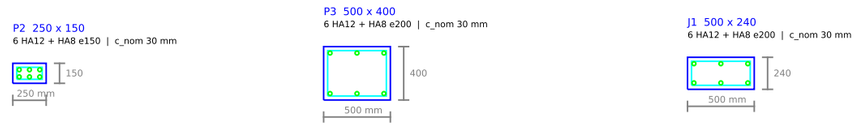

2. COUPE P2 — fût 150x250 x H=2800 mm (HYPOTHESE B-20 / R-42-1) — ech. 1/20 — cotes mm

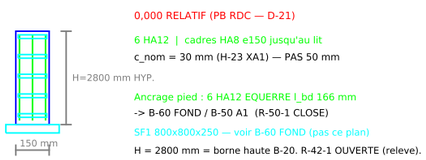

D-34 — MAÇONNERIE (mot pour mot, plan ET note) :

f_k = 1,5 MPa · f_vk0 = 0,15 MPa. Essais hors mission.

Si non concluants : reprise d'étude chiffrée. J1 : sigma_d = 0,332 MPa (0,55 à f_k=1,5 ; défaut si f_k < 0,83).

Dé de répartition sous J1 : option B-46, pas une initiative de ce plan. R-42-3 OUVERTE.

D-19 : pieds P3 et J1 = nuages (vérif. soubassement à l'ouverture des fouilles). P2 CERTAIN sur SF1.

D-26 : AUCUNE vérification sismique. D-28 : AUCUN joint de dilatation.

R-42-1 : H non relevée. R-42-2 : excentricité F2/P2 → B-50. Feu : ADEQUATE A PREVOIR (hors lot GO).

3. NOMENCLATURE GRAPHIQUE (faconnage -> B-62)

P2 150x250 C25/30 x1 | 6 HA12 S500B | cadres HA8 e150 | N_Ed 159,0 kN | CERTAIN

P3 400x500 C25/30 x1 | 6 HA12 S500B | cadres HA8 e200 | N_Ed 35,8 kN | D-19

J1 240x500 C25/30 x1 | 6 HA12 S500B | cadres HA8 e200 | N_Ed 39,8 kN | D-19 / D-34

H = 2800 mm HYPOTHESE B-20 — debits indicatifs (B-62). P1-N/S, R1/R2/R3, F2/F3 : hors type.

EHPAD LA ROSERAIE — PAVILLON FLORA (CROISSY-SUR-SEINE)

B-60 VERT EXE · Ind. A · 21/10/2026 · PARTIEL-DECLARE · fond B-32 D · amont B-42 B

NE PAS EXECUTER SANS EXE COTE ET VISA

Protection au feu : ADEQUATE A PREVOIR (hors lot GO) · CARNAC v3.0 · cotes mm · DXF cm