
CROISSY-FLORA — B-60 Ind. A — LINTEAUX EXE COTÉS (F1a/b/c · R3-N/S)
NE PAS EXÉCUTER SANS EXE COTÉ ET VISA (Fond B-32 Ind. D · S1 hors bois)

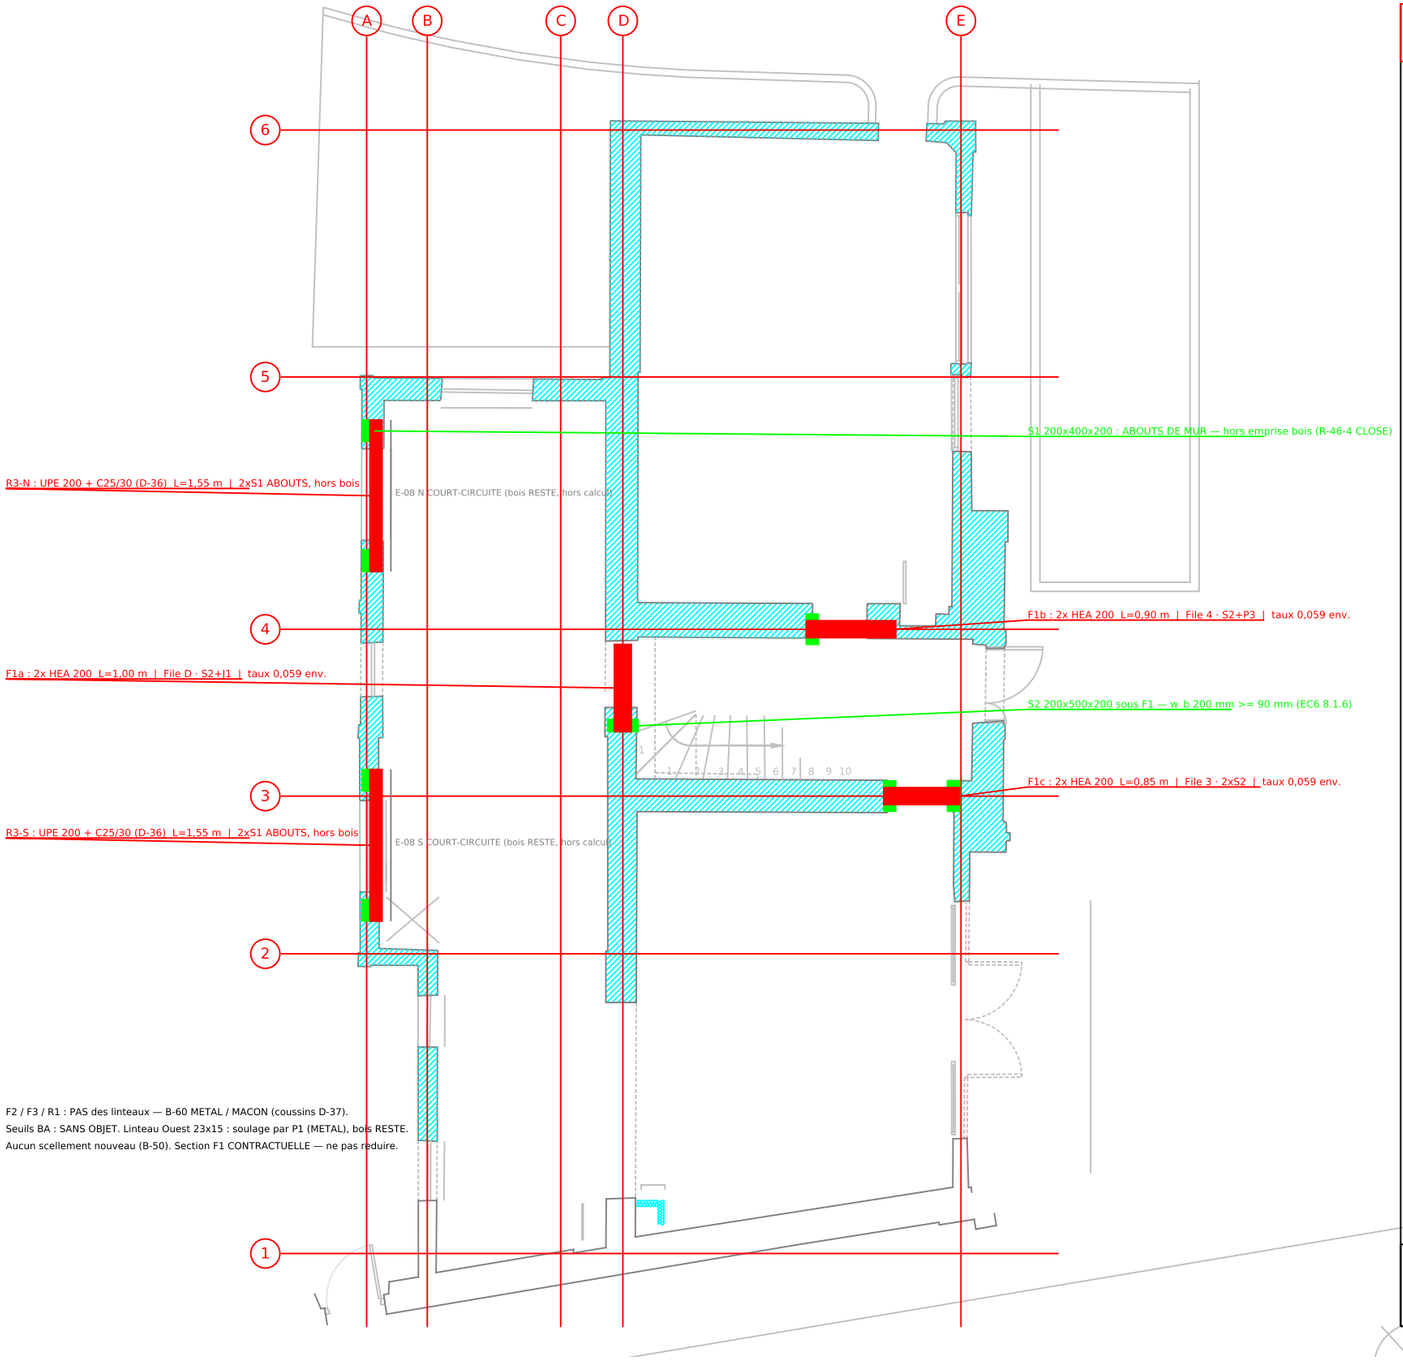

F2 / F3 / R1 : PAS des linteaux — B-60 METAL / MACON (coussins D-37).
Seuils BA : SANS OBJET. Linteau Ouest 23x15 : soulage par P1 (METAL), bois RESTE.
Aucun scellement nouveau (B-50). Section F1 CONTRACTUELLE — ne pas reduire.

B-60 Ind. A | LINTEAU EXE | F1a/b/c + R3-N/S IMPLANTES | NE PAS EXECUTER SANS EXE COTE ET VISA

1. SECTIONS — cotes mm — S275 — ne pas reduire F1 (D2 f.01)

F1a/b/c : 2 x HEA 200 S275
h=190 b=200 | M_Rd 236 kN.m | taux env. 0,059




Appui S2 200x500x200 | triangle 60 deg OK 0,010

R3-N/S : UPE 200 + remplissage C25/30 (D-36)
L_baie 1550 mm | M_Ed 17,9 / 61,6 = 0,291 | torsion CLOSE



Detail de coulage du remplissage -> B-60 METAL

2. COTATION S1 HORS BOIS — R-46-4 — cotes mm

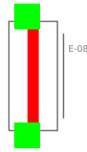

S1 200 x 400 x 200 mm — ABOUT de mur
Hors emprise du linteau bois. Aucun sommier sur E-08.
R3 UPE 200 L_baie = 1550 mm (profilé livré 2500 mm)
Remplissage C25/30 entre ailes — D-36 — R-50-2 CLOSE

2 x S1 par linteau. w_b = 200 mm. Coussin D-37 NON requis sur R3.

D-34 — MAÇONNERIE (mot pour mot, plan ET note) : f_k = 1,5 MPa · f_vk0 = 0,15 MPa.

Essais hors mission. Si non concluants : reprise d'étude chiffrée.

D-36 : UPE 200 de R3 REMPLI C25/30. D-26 : AUCUNE vérif. sismique. D-28 : AUCUN joint de dilatation.

D-37 (coussins R1/F2/F3) : PAS des linteaux — B-60 MACON. Feu : ADEQUATE A PREVOIR (hors lot GO).

E-08 : court-circuité. Aucun relevé de bois (non prescrit). Seuils BA : SANS OBJET.

3. NOMENCLATURE GRAPHIQUE (faconnage -> B-62)

F1a 2xHEA 200 L=1000 x1 | S2 200x500x200 | File D | taux 0,010 / 0,059

F1b 2xHEA 200 L= 900 x1 | S2 + P3 | File 4 | taux 0,008 / 0,059

F1c 2xHEA 200 L= 850 x1 | 2x S2 | File 3 | taux 0,007 / 0,059

R3-N UPE 200 + C25/30 L_baie=1550 x1 | 2x S1 ABOUTS | 0,291 | D-36

R3-S UPE 200 + C25/30 L_baie=1550 x1 | 2x S1 ABOUTS | 0,291 | D-36

S1 x4 (R3) 200x400x200 C25/30 | S2 x4 (F1) 200x500x200 C25/30 | S275 profilés

EHPAD LA ROSERAIE — PAVILLON FLORA (CROISSY-SUR-SEINE)
B-60 LINTEAU EXE · Ind. A · 21/10/2026 · PARTIEL-DECLARE · fond B-32 D · amont B-49 A
NE PAS EXECUTER SANS EXE COTE ET VISA
Protection au feu : ADEQUATE A PREVOIR (hors lot GO) · CARNAC v3.0 · cotes mm · DXF cm