
MONSIEUR ET MADAME DANIEL LEON - GUJAN-MESTRAS - CONSTRUCTION D'UNE RESIDENCE PRINCIPALE


CONTROLE DIMENSIONNEL DU CALAGE

Chaine haute du document : 17 + 300 + 17 + 350 + 7 + 66 + 7
+ 85 + 7 + 200 + 7 + 418 + 25 = 1506 cm (fermeture exacte)
Profondeur : 7.00 m hors-oeuvre, 6.66 m interieur.
Surfaces retrouvees exactement : GARAGE 19.98, CHAMBRE 1 11.83, CUISINE 10.50, PLACARD 0.96, W.C. 1.36, ENTREE 8.91, ESCALIER 2.43, TERRASSE 28.60.
Surfaces legerement differentes (relevé non cotable sur la photo) : SEJOUR (30.17), BAINS (7.14), DEGAGEMENT (1.89), VESTIAIRE (0.98).
Points a verifier sur l'original : position exacte de la cloison separatrice (cote 2.69 lue) et limite de la terrasse au sud (cote 2.30).

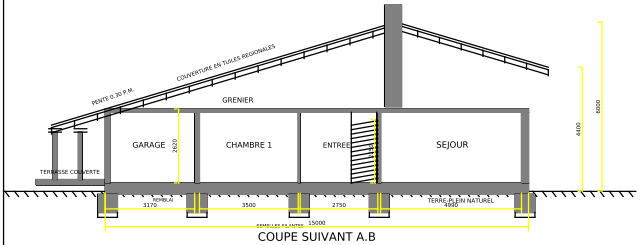

COUPE SUIVANT A.B

ECHELLE 0.02 P.M. (1/50)

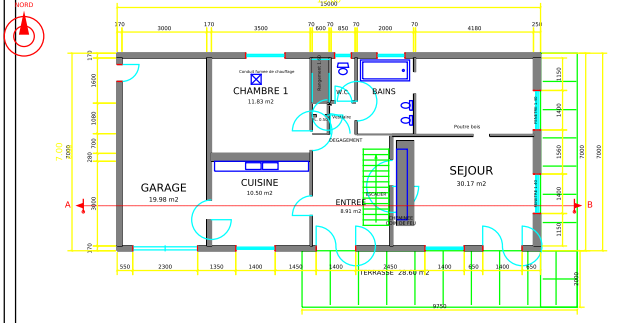

PLAN DU REZ-DE-CHAUSSEE

ECHELLE 0.02 P.M. (1/50)

SURFACES (m2) - valeurs portees au cartouche d'origine

PIECE	CART.	DESSIN
SEJOUR	30.17	30,69
ENTREE	8.91	9.05
DEGAGEMENT	1.89	1,90
PLACARD	0.30	0,32
VESTIAIRE	0.98	0,98
BAINS	7.14	5,61
W.C.	1.36	1,36
CUISINE	10.50	10,50
CHAMBRE 1	11.83	11,83
PLACARD	0.96	0,96
GARAGE	19.98	19,98
ESCALIER	-	2,43
TOTAL	91.59	95.61
TERRASSE 28.60	|	28,60

ETAGE (combles) - planche non fournie

DEGAGEMENT	1.88
PLACARD	0.40
TOILETTE	1.40
CHAMBRE 2	11.97
PLACARD	1.20
CHAMBRE 3	14.75
PLACARD	1.20
GRENIER	35.90
ESCALIER	2.43
BALCON	4.40

NOTE : la coupe et les surfaces sont celles portees au document d'origine.
Les cotes grises du dessin sont recalculees sur la geometrie reconstruite.

MENUISERIES EXTERIEURES

N.	DESIGNATION	L x H (m)	FAC.
1	Porte de garage basculante	2.90 x 2.10	S
2	Porte de service (garage)	0.90 x 2.10	O
3	Fenetre cuisine	1.40 x 1.00	S
4	Baie coulissante 2 vantaux	2.40 x 2.20	S
5	Fenetre sejour	1.40 x 1.00	S
6	Porte-fenetre sejour	1.40 x 2.10	S
7	Fenetre chambre 1	1.40 x 1.00	N
8	Fenetre W.C.	0.80 x 0.60	N
9	Fenetre bains	1.00 x 0.60	N
10	Chassis sejour est (x2)	1.40 x 1.00	E

Dimensions a verifier sur l'original (non cotees).

LEGENDE

- Murs exterieurs porteurs (0.17 m)
- Cloisons et refends (0.07 m)
- Baies - tableaux et ebrasements
- Menuiseries, portes, debattements
- Escalier (14 marches, 0.90 m)
- Appareils sanitaires, evier, conduit
- Dallage de terrasse (28.60 m2)
- Cotation (metres)
- Coupe A-B (murs, planchers, toiture)

MONSIEUR ET MADAME DANIEL LEON PROPRIETAIRES - LOTISSEMENT CHANTE CIGALE L.T 77 GUJAN-MESTRAS - GIRONDE	
CONSTRUCTION D'UNE RESIDENCE PRINCIPALE PLAN - COUPE - SURFACES	ECHELLE 0.02 P.M. = 1/50
ENTREPRISE GRAND S.A.R.L. au Capital de 20.000 F. LE CANON - 33151 R.C. 73 B 213 - Telephone 60.53.29 DESSINE J. GRAND - JUIN 1975	PLANCHE 01 / 01 INDICE A Retranscription vectorielle (DAO)

Retranscription DXF de la planche du permis de construire (plan / coupe / surfaces) - unites mm - echelle 1/50